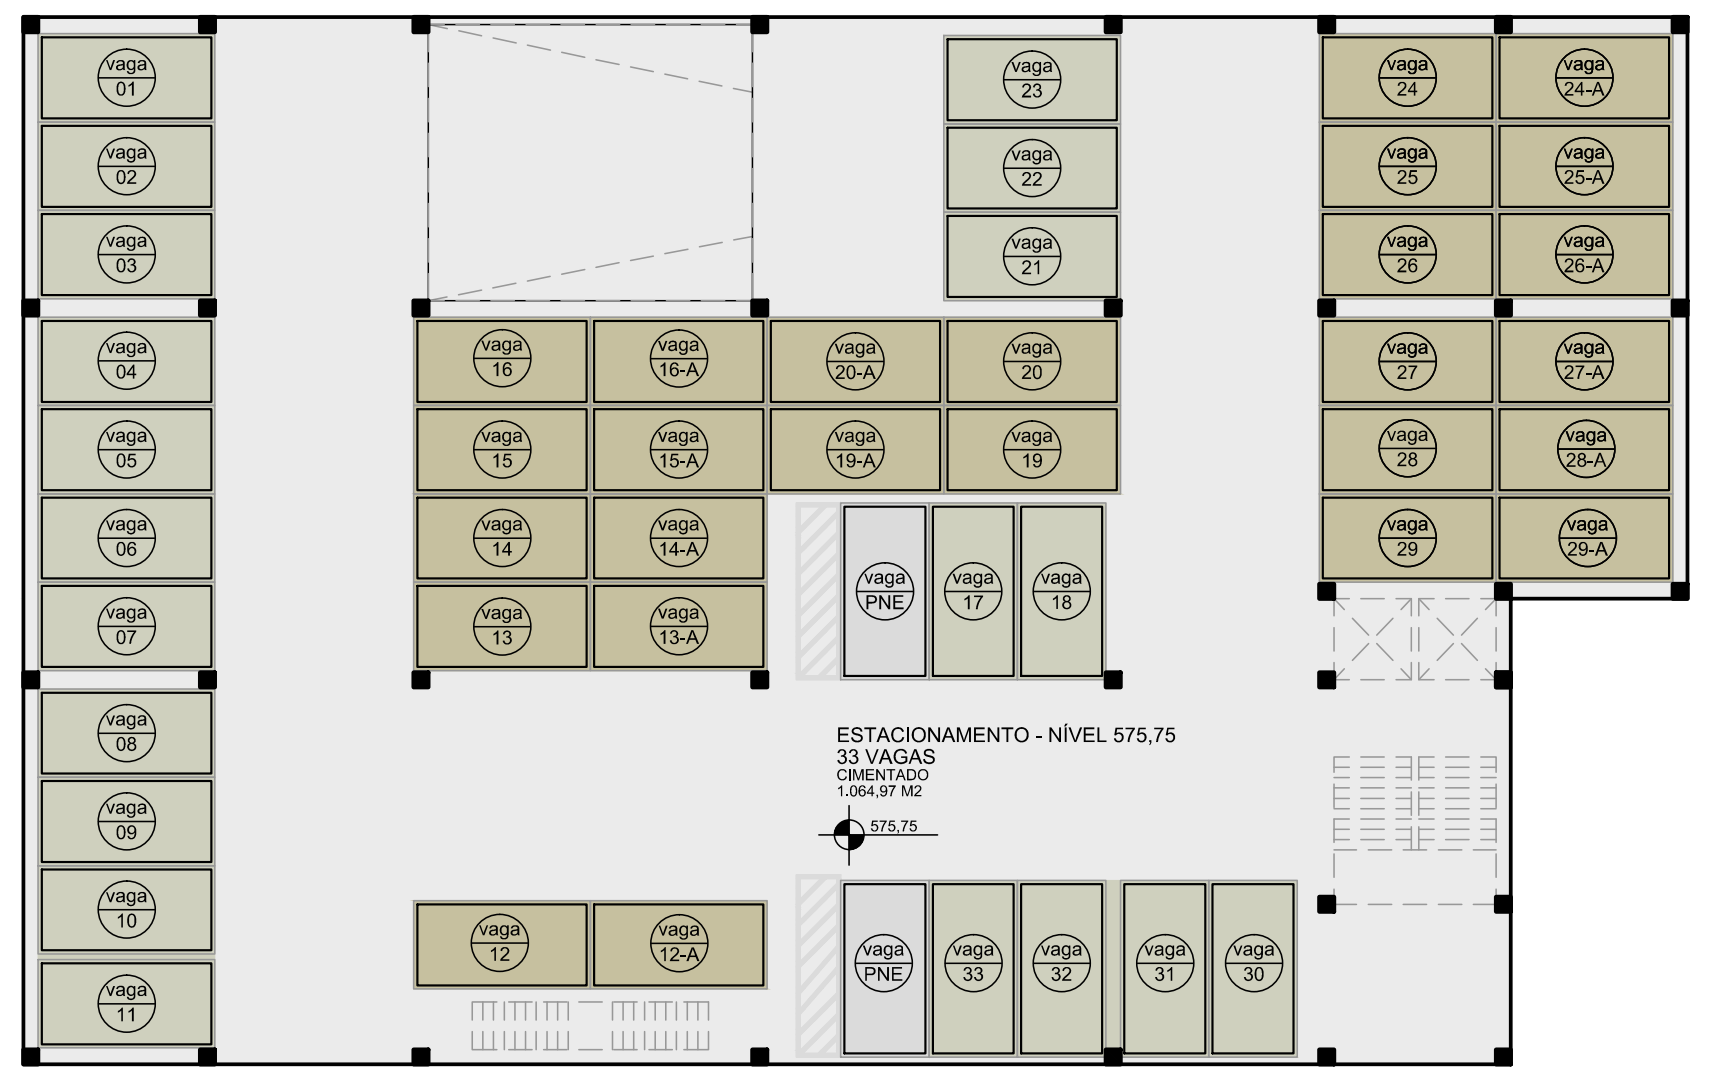

MEMORIAL ESTACIONAMENTO NÍVEL 575,75 (PRANCHA 02)

ESC. 1:200

TOTAL DE VAGAS COMUNS.. 20 VAGAS
TOTAL DE VAGAS DUPLAS.. 13 VAGAS
TOTAL DE VAGAS PNE.. 02 VAGAS
TOTAL DE VAGAS NO PAVIMENTO..................................... 33 VAGAS + 2 VAGAS PNE

LEGENDA:

🟩	VAGAS COMUNS
🟫	VAGAS DUPLAS
⬜	VAGAS PNE

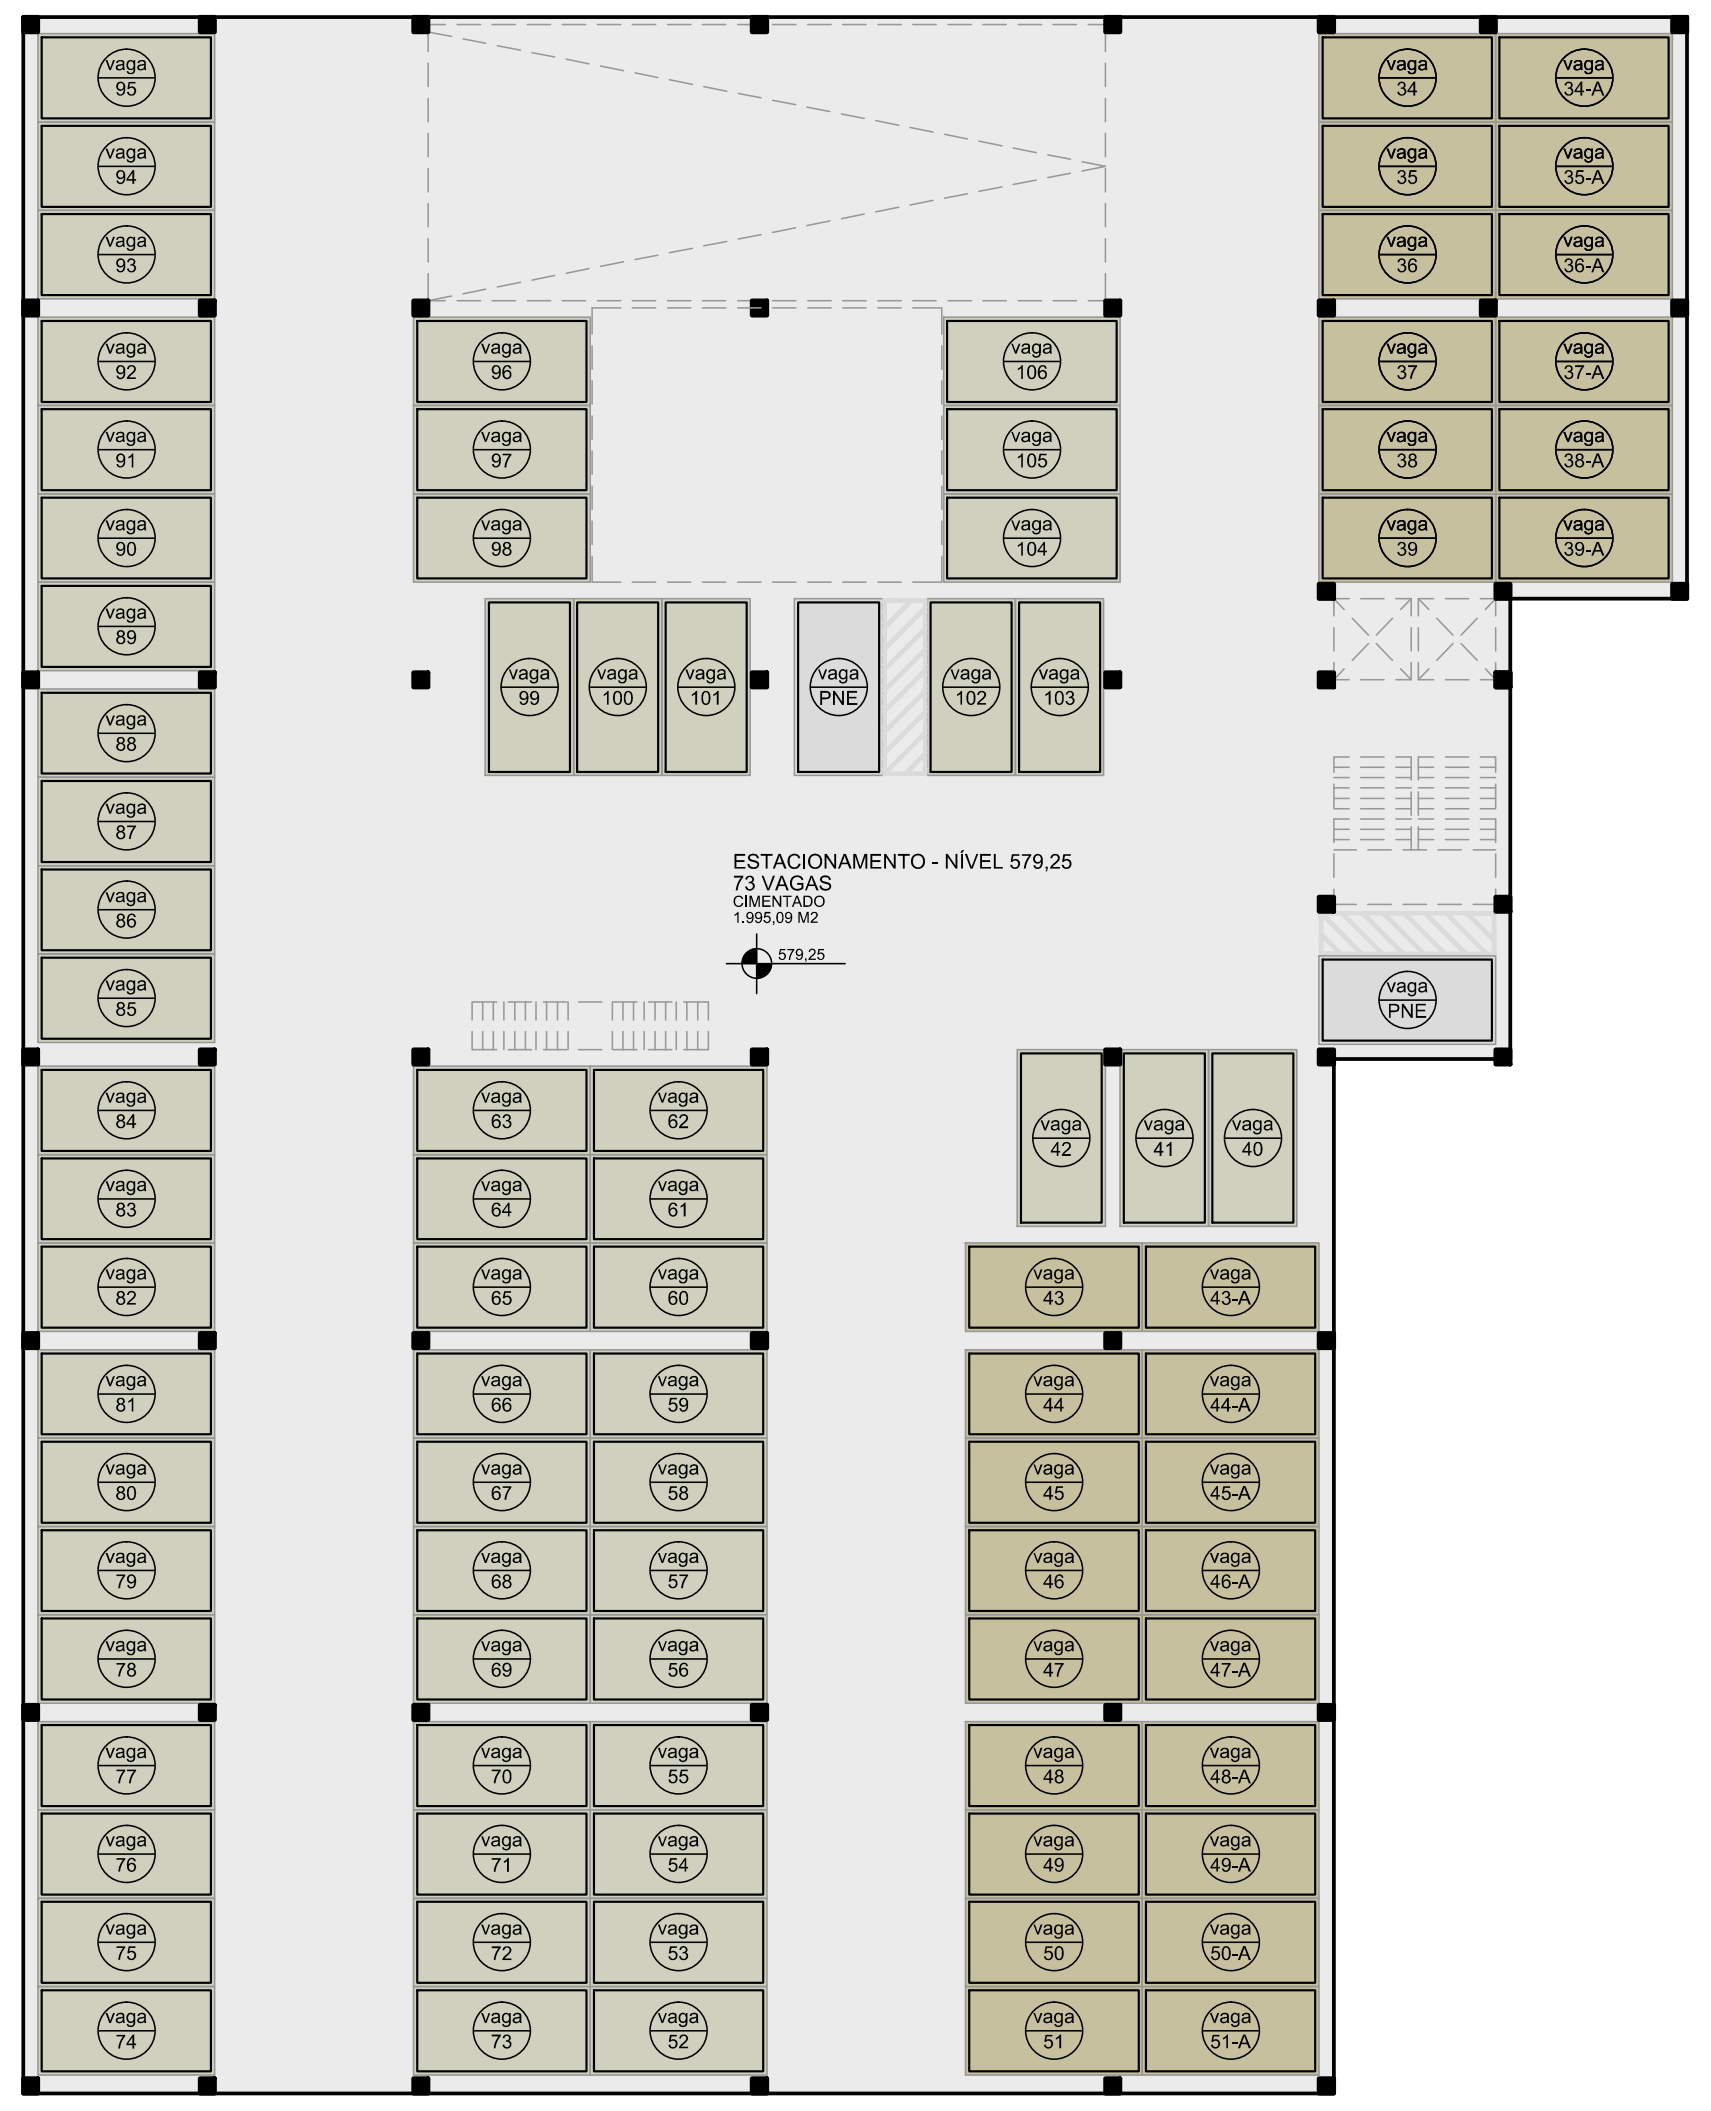

MEMORIAL ESTACIONAMENTO NÍVEL 579,25 (PRANCHA 02

ESC. 1:200

TOTAL DE VAGAS COMUNS.. 58 VAGAS
TOTAL DE VAGAS DUPLAS.. 15 VAGAS
TOTAL DE VAGAS PNE.. 02 VAGAS
TOTAL DE VAGAS NO PAVIMENTO..................................... 73 VAGAS + 2 VAGAS PNE

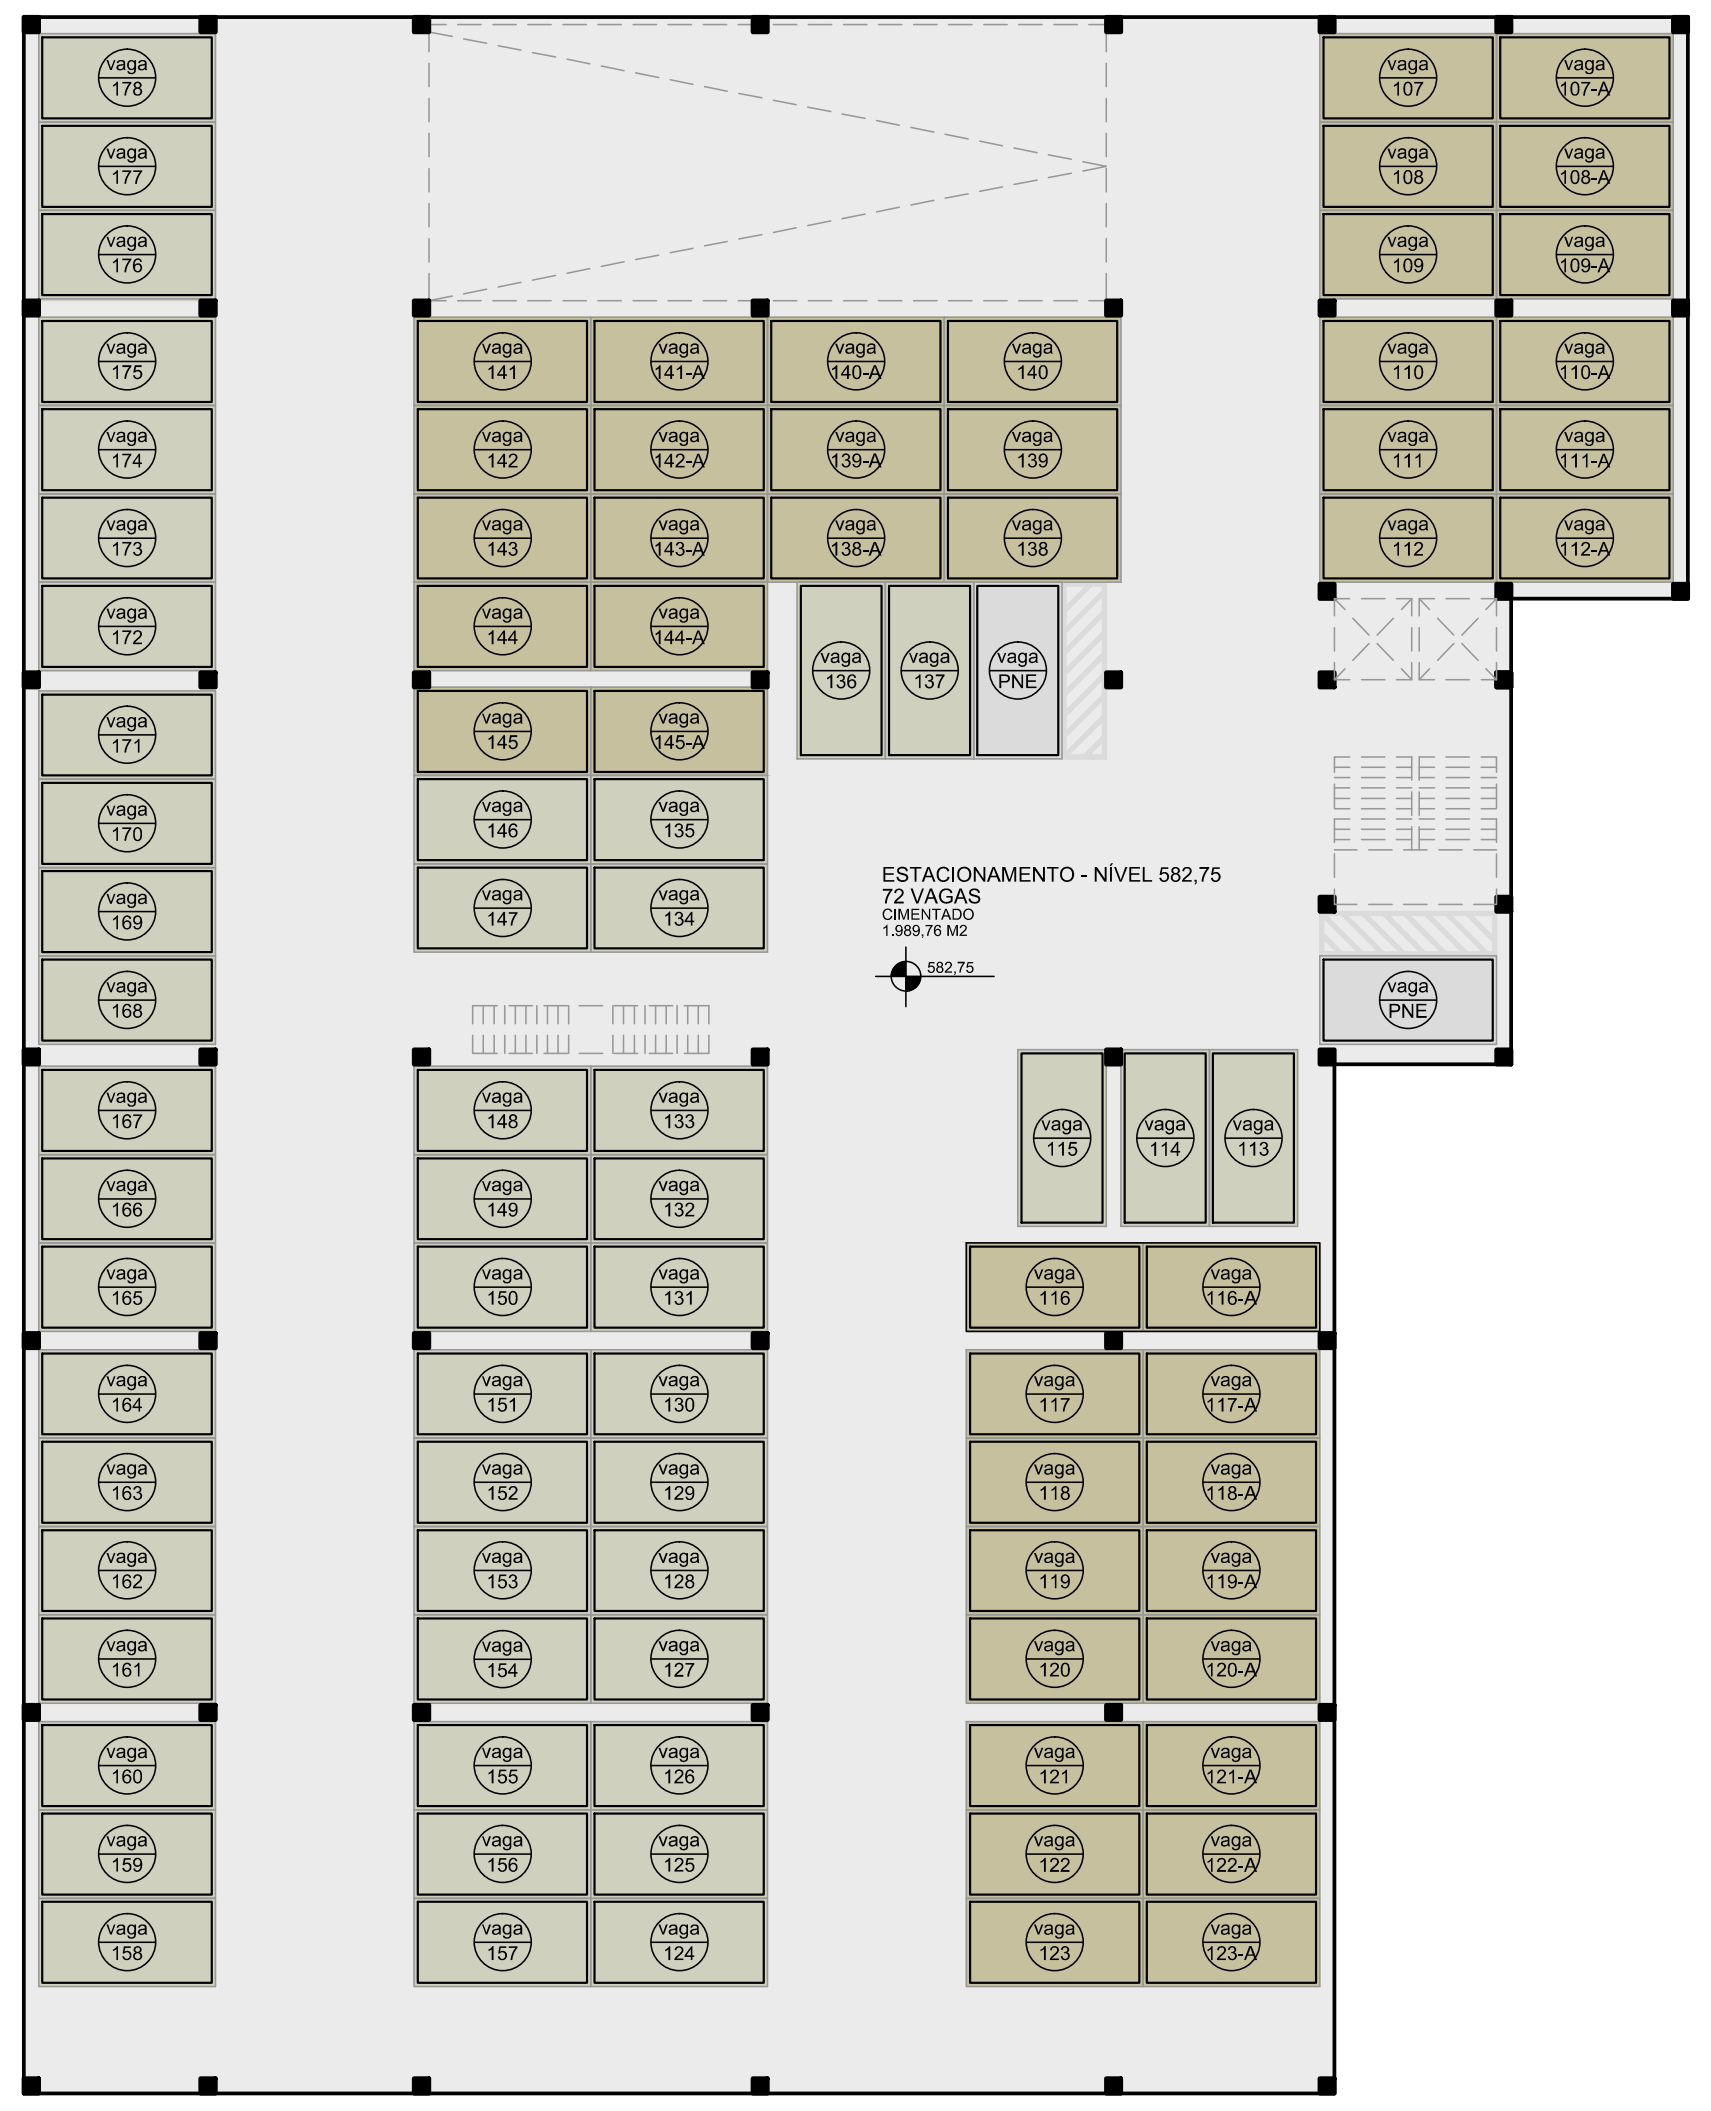

MEMORIAL ESTACIONAMENTO NÍVEL 582,75 (PRANCHA 01)

ESC. 1:200

TOTAL DE VAGAS COMUNS.. 50 VAGAS
TOTAL DE VAGAS DUPLAS.. 22 VAGAS
TOTAL DE VAGAS PNE.. 02 VAGAS
TOTAL DE VAGAS NO PAVIMENTO..................................... 72 VAGAS + 2 VAGAS PNE

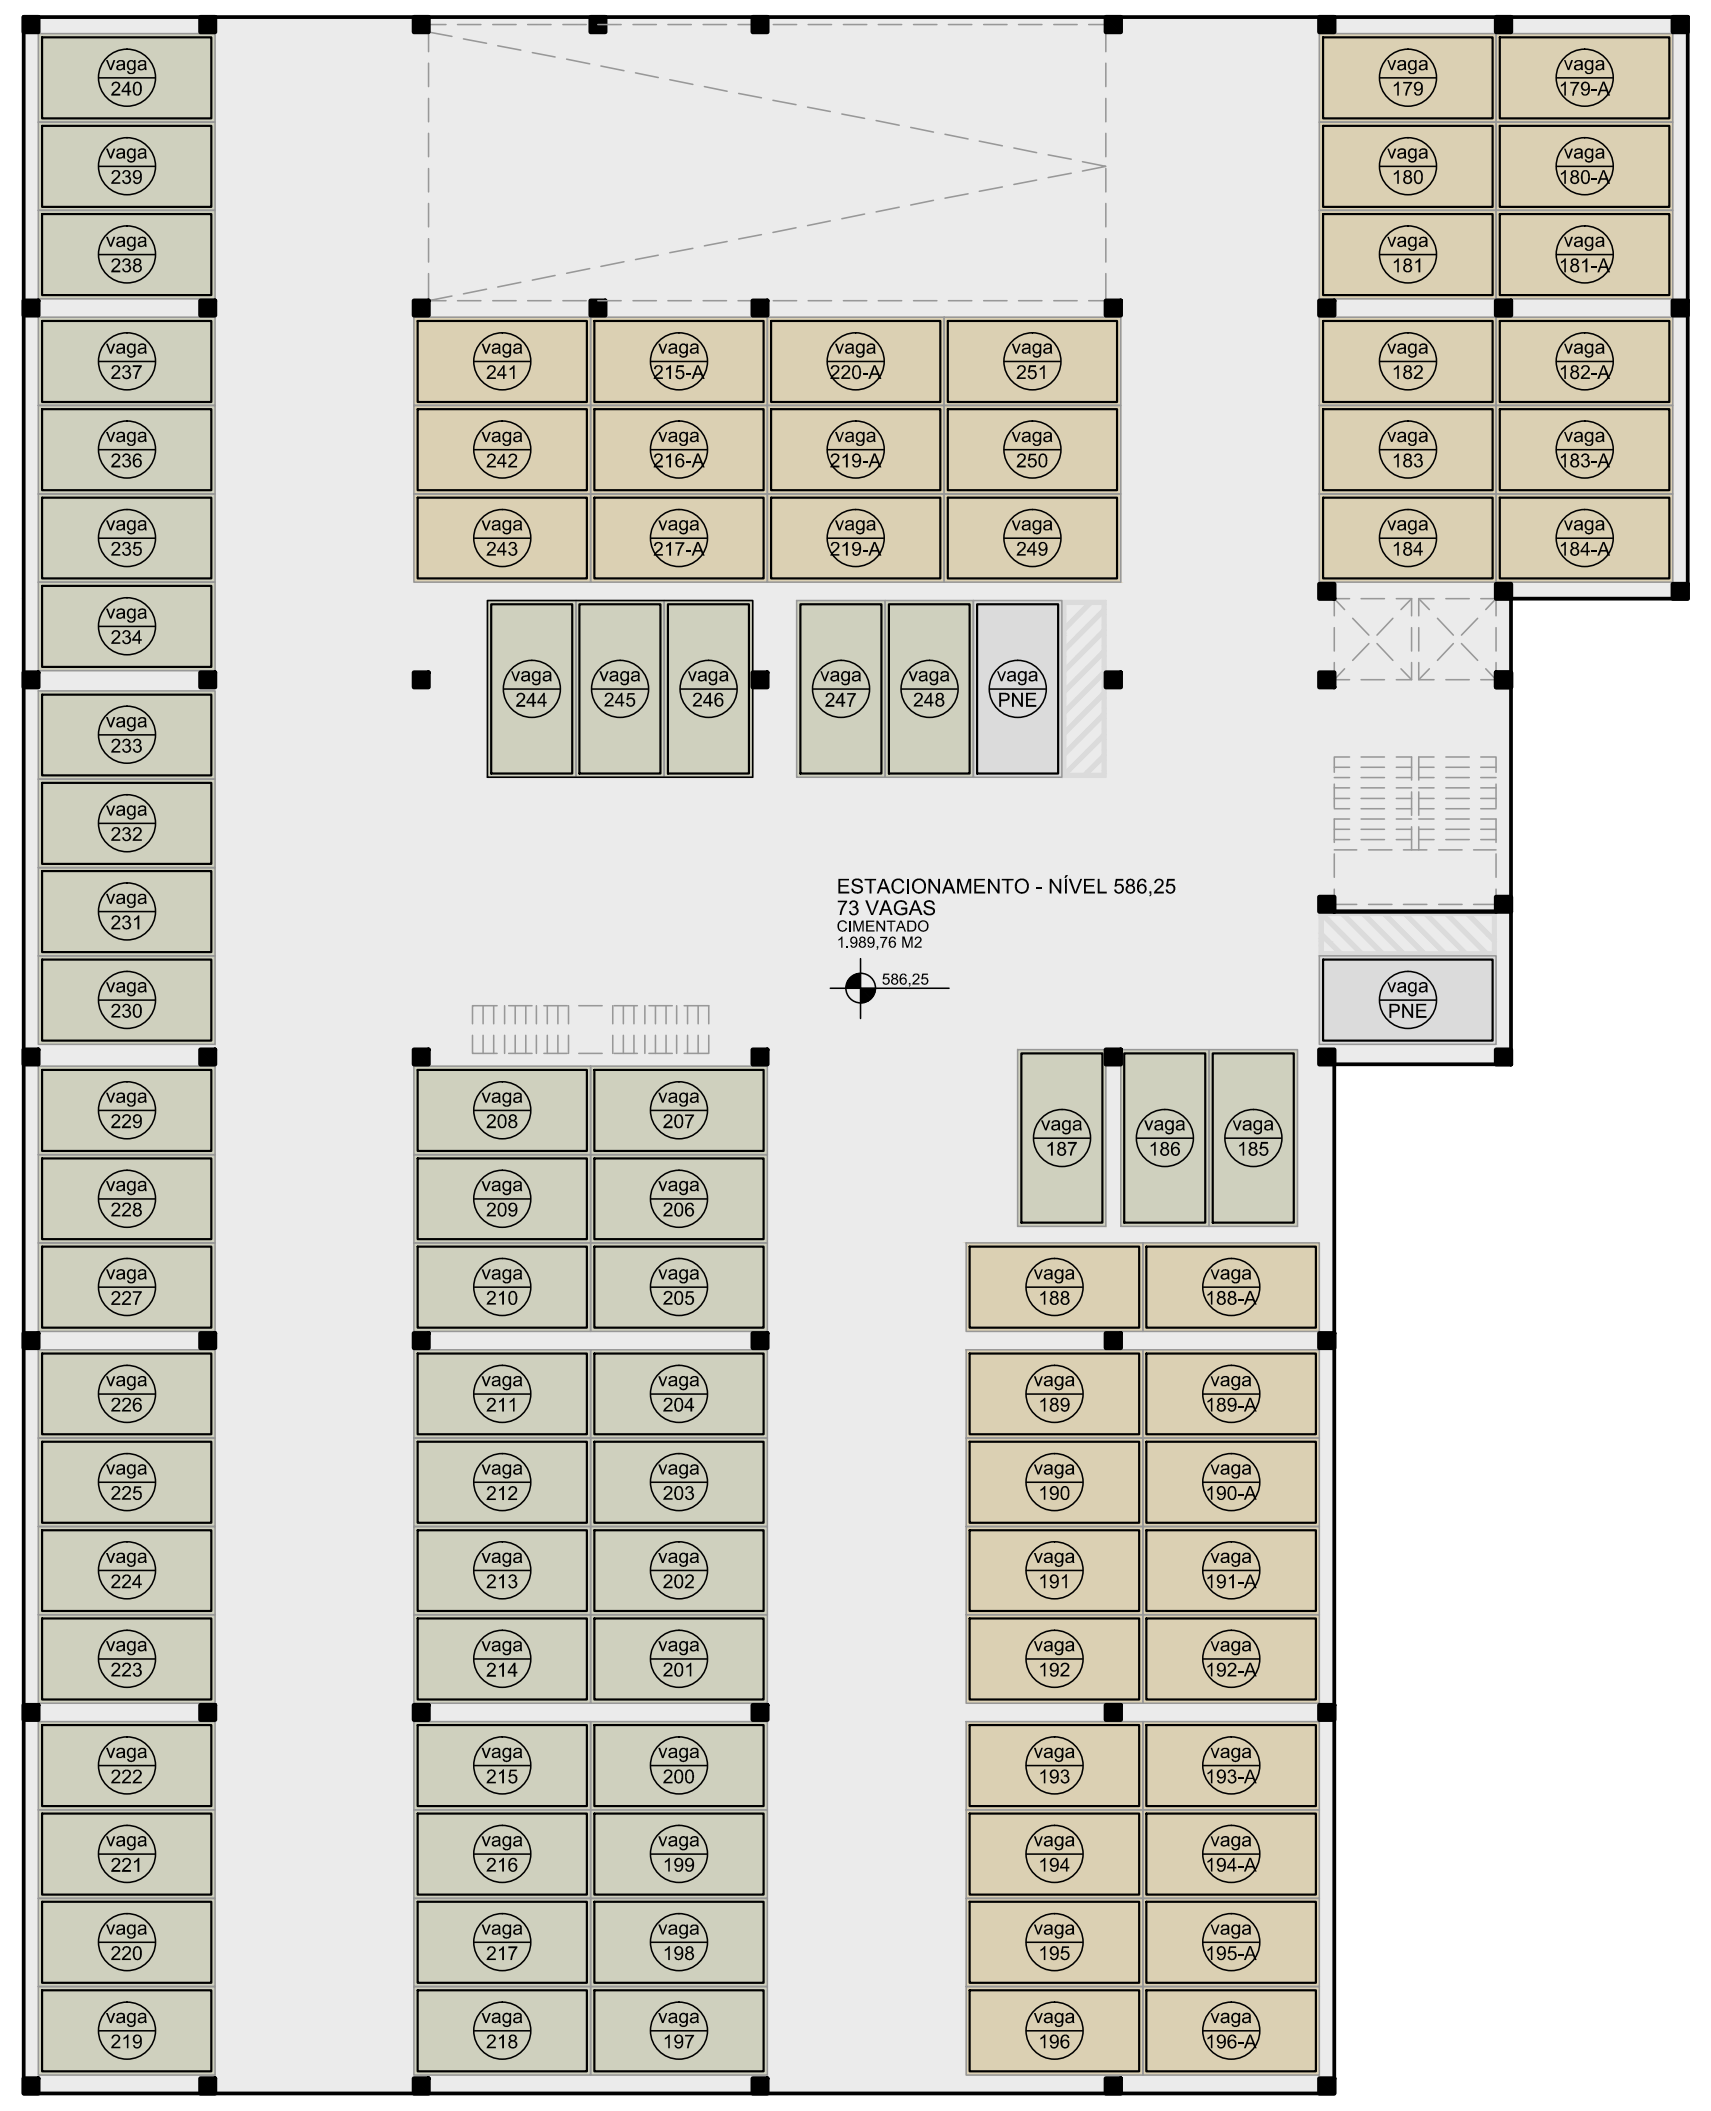

MEMORIAL ESTACIONAMENTO NÍVEL (PRANCHA 03)

ESC. 1:200

TOTAL DE VAGAS COMUNS.. 52 VAGAS
TOTAL DE VAGAS DUPLAS.. 21 VAGAS
TOTAL DE VAGAS PNE.. 02 VAGAS
TOTAL DE VAGAS NO PAVIMENTO..................................... 73 VAGAS + 2 VAGAS PNE

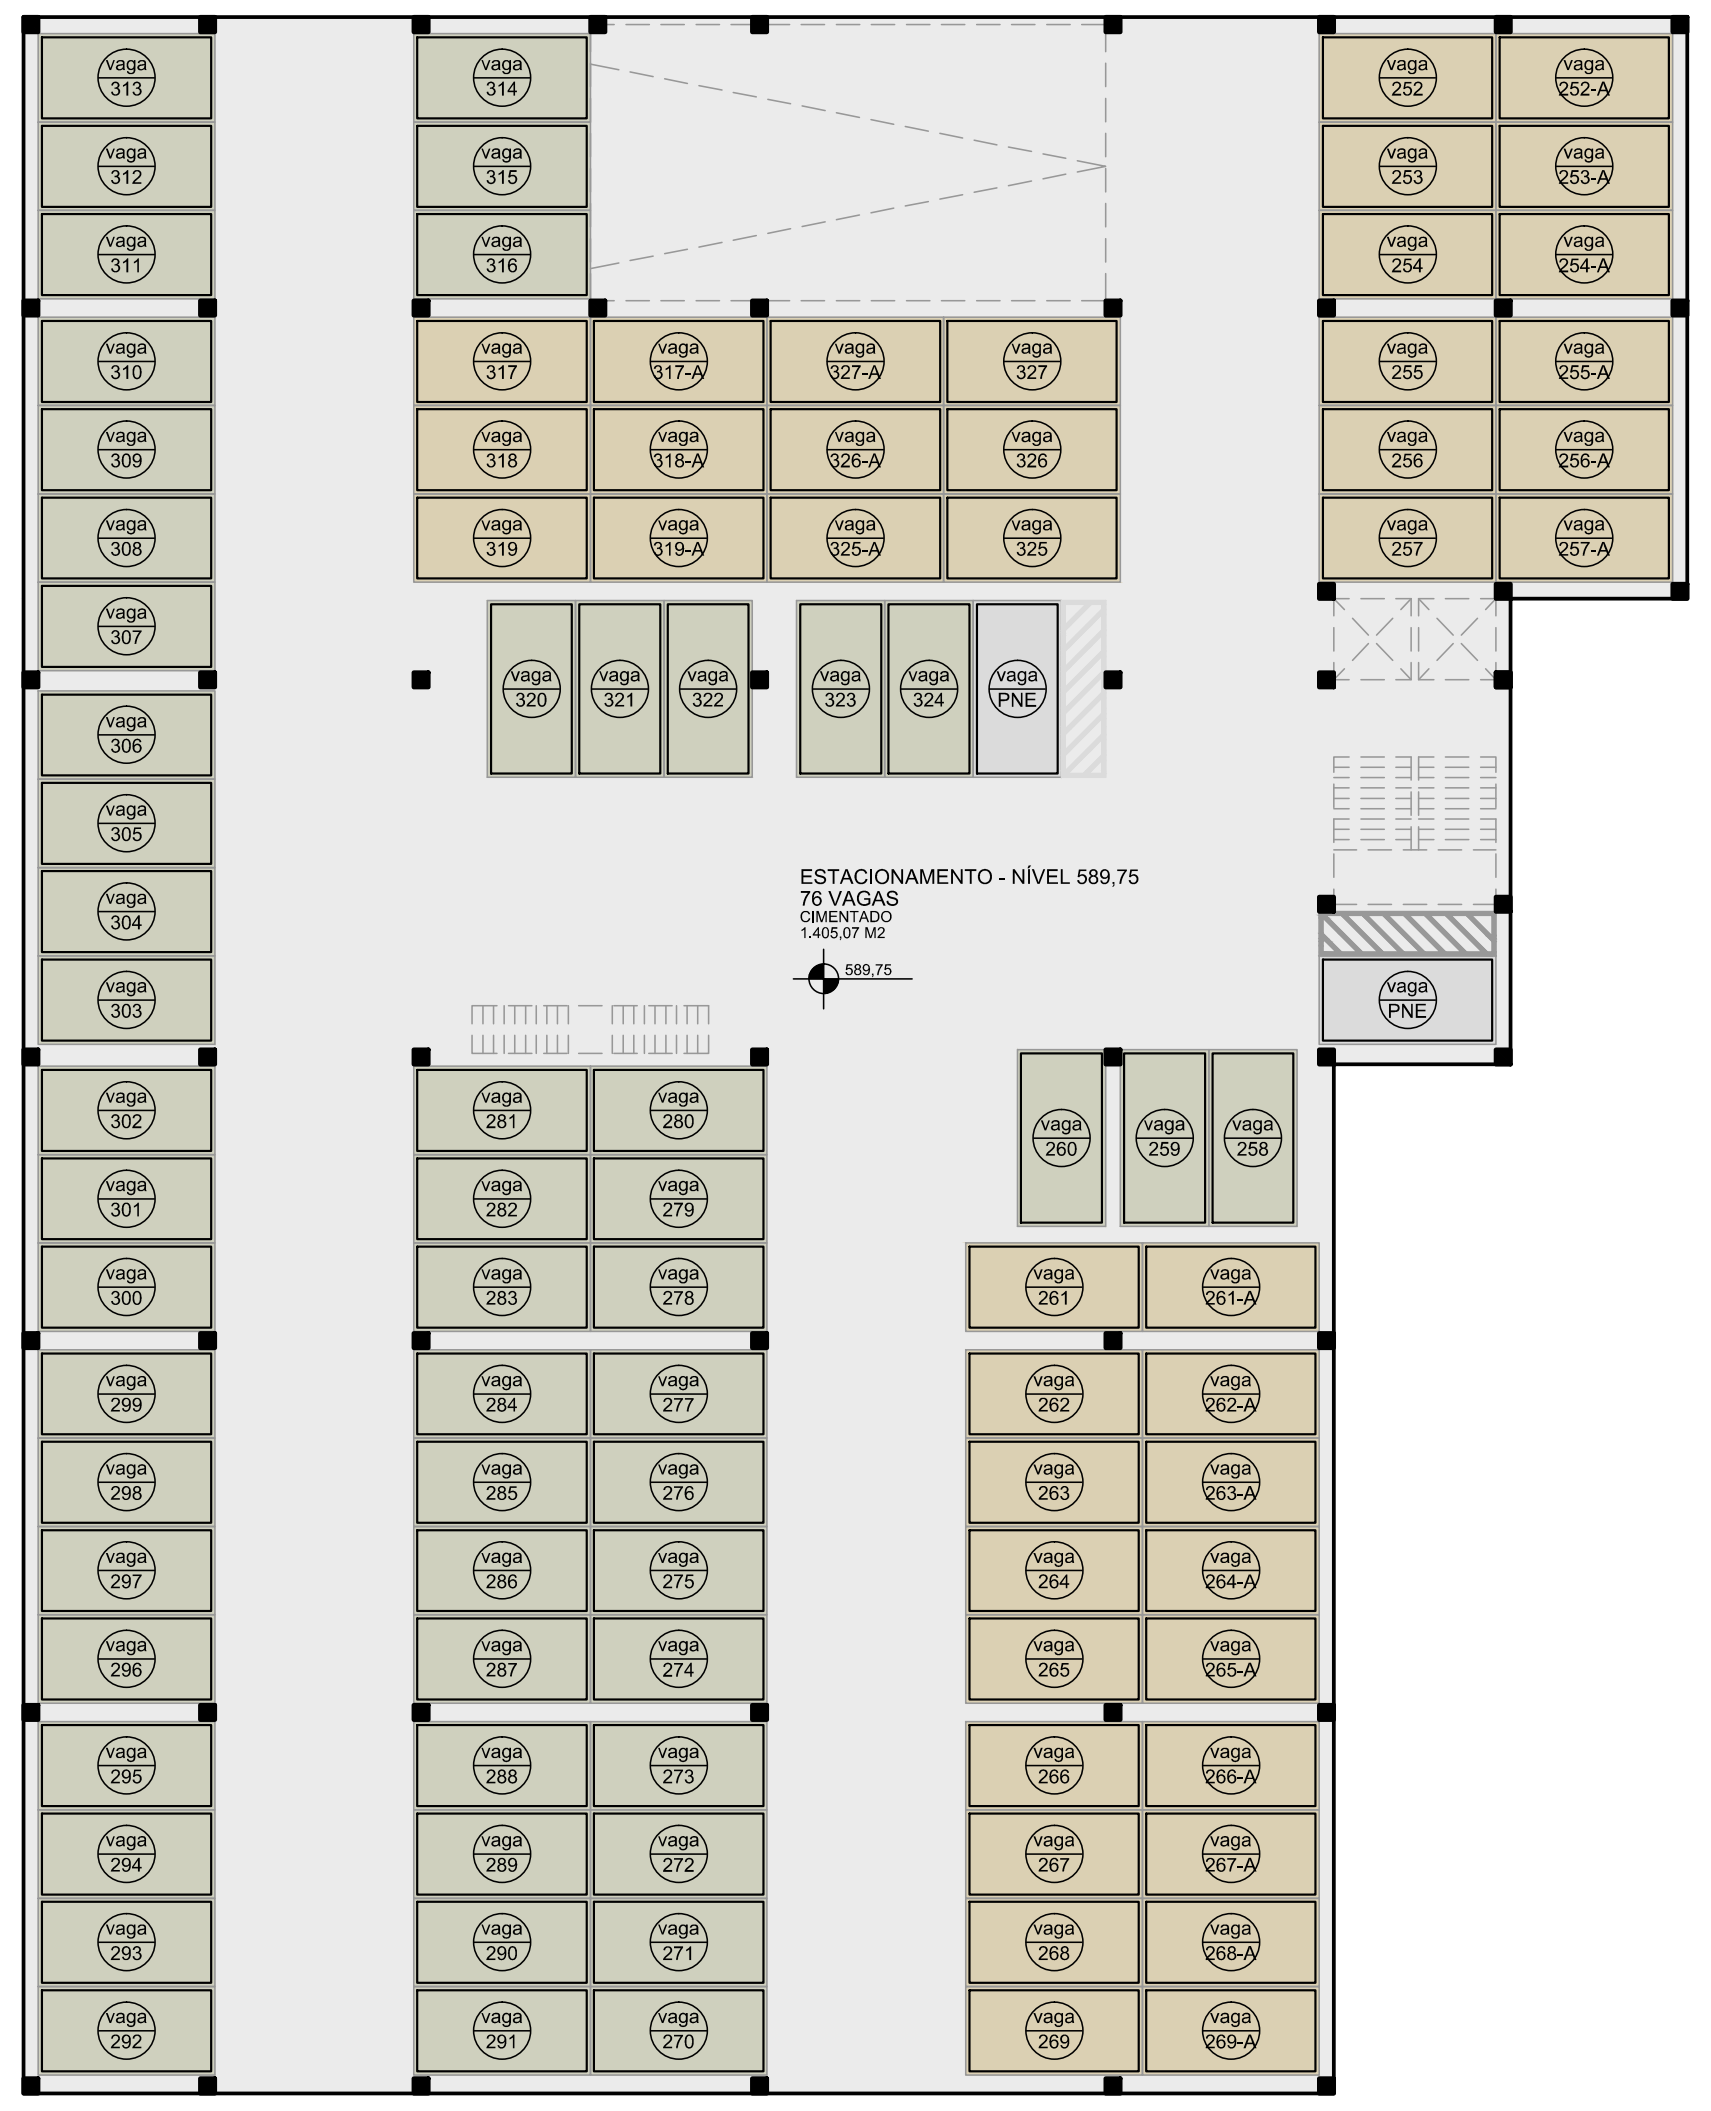

MEMORIAL ESTACIONAMENTO NÍVEL 589,75 (PRANCHA 03)

ESC. 1:200

TOTAL DE VAGAS COMUNS.. 55 VAGAS
TOTAL DE VAGAS DUPLAS.. 21 VAGAS
TOTAL DE VAGAS PNE.. 02 VAGAS
TOTAL DE VAGAS NO PAVIMENTO..................................... 76 VAGAS + 2 VAGAS PNE

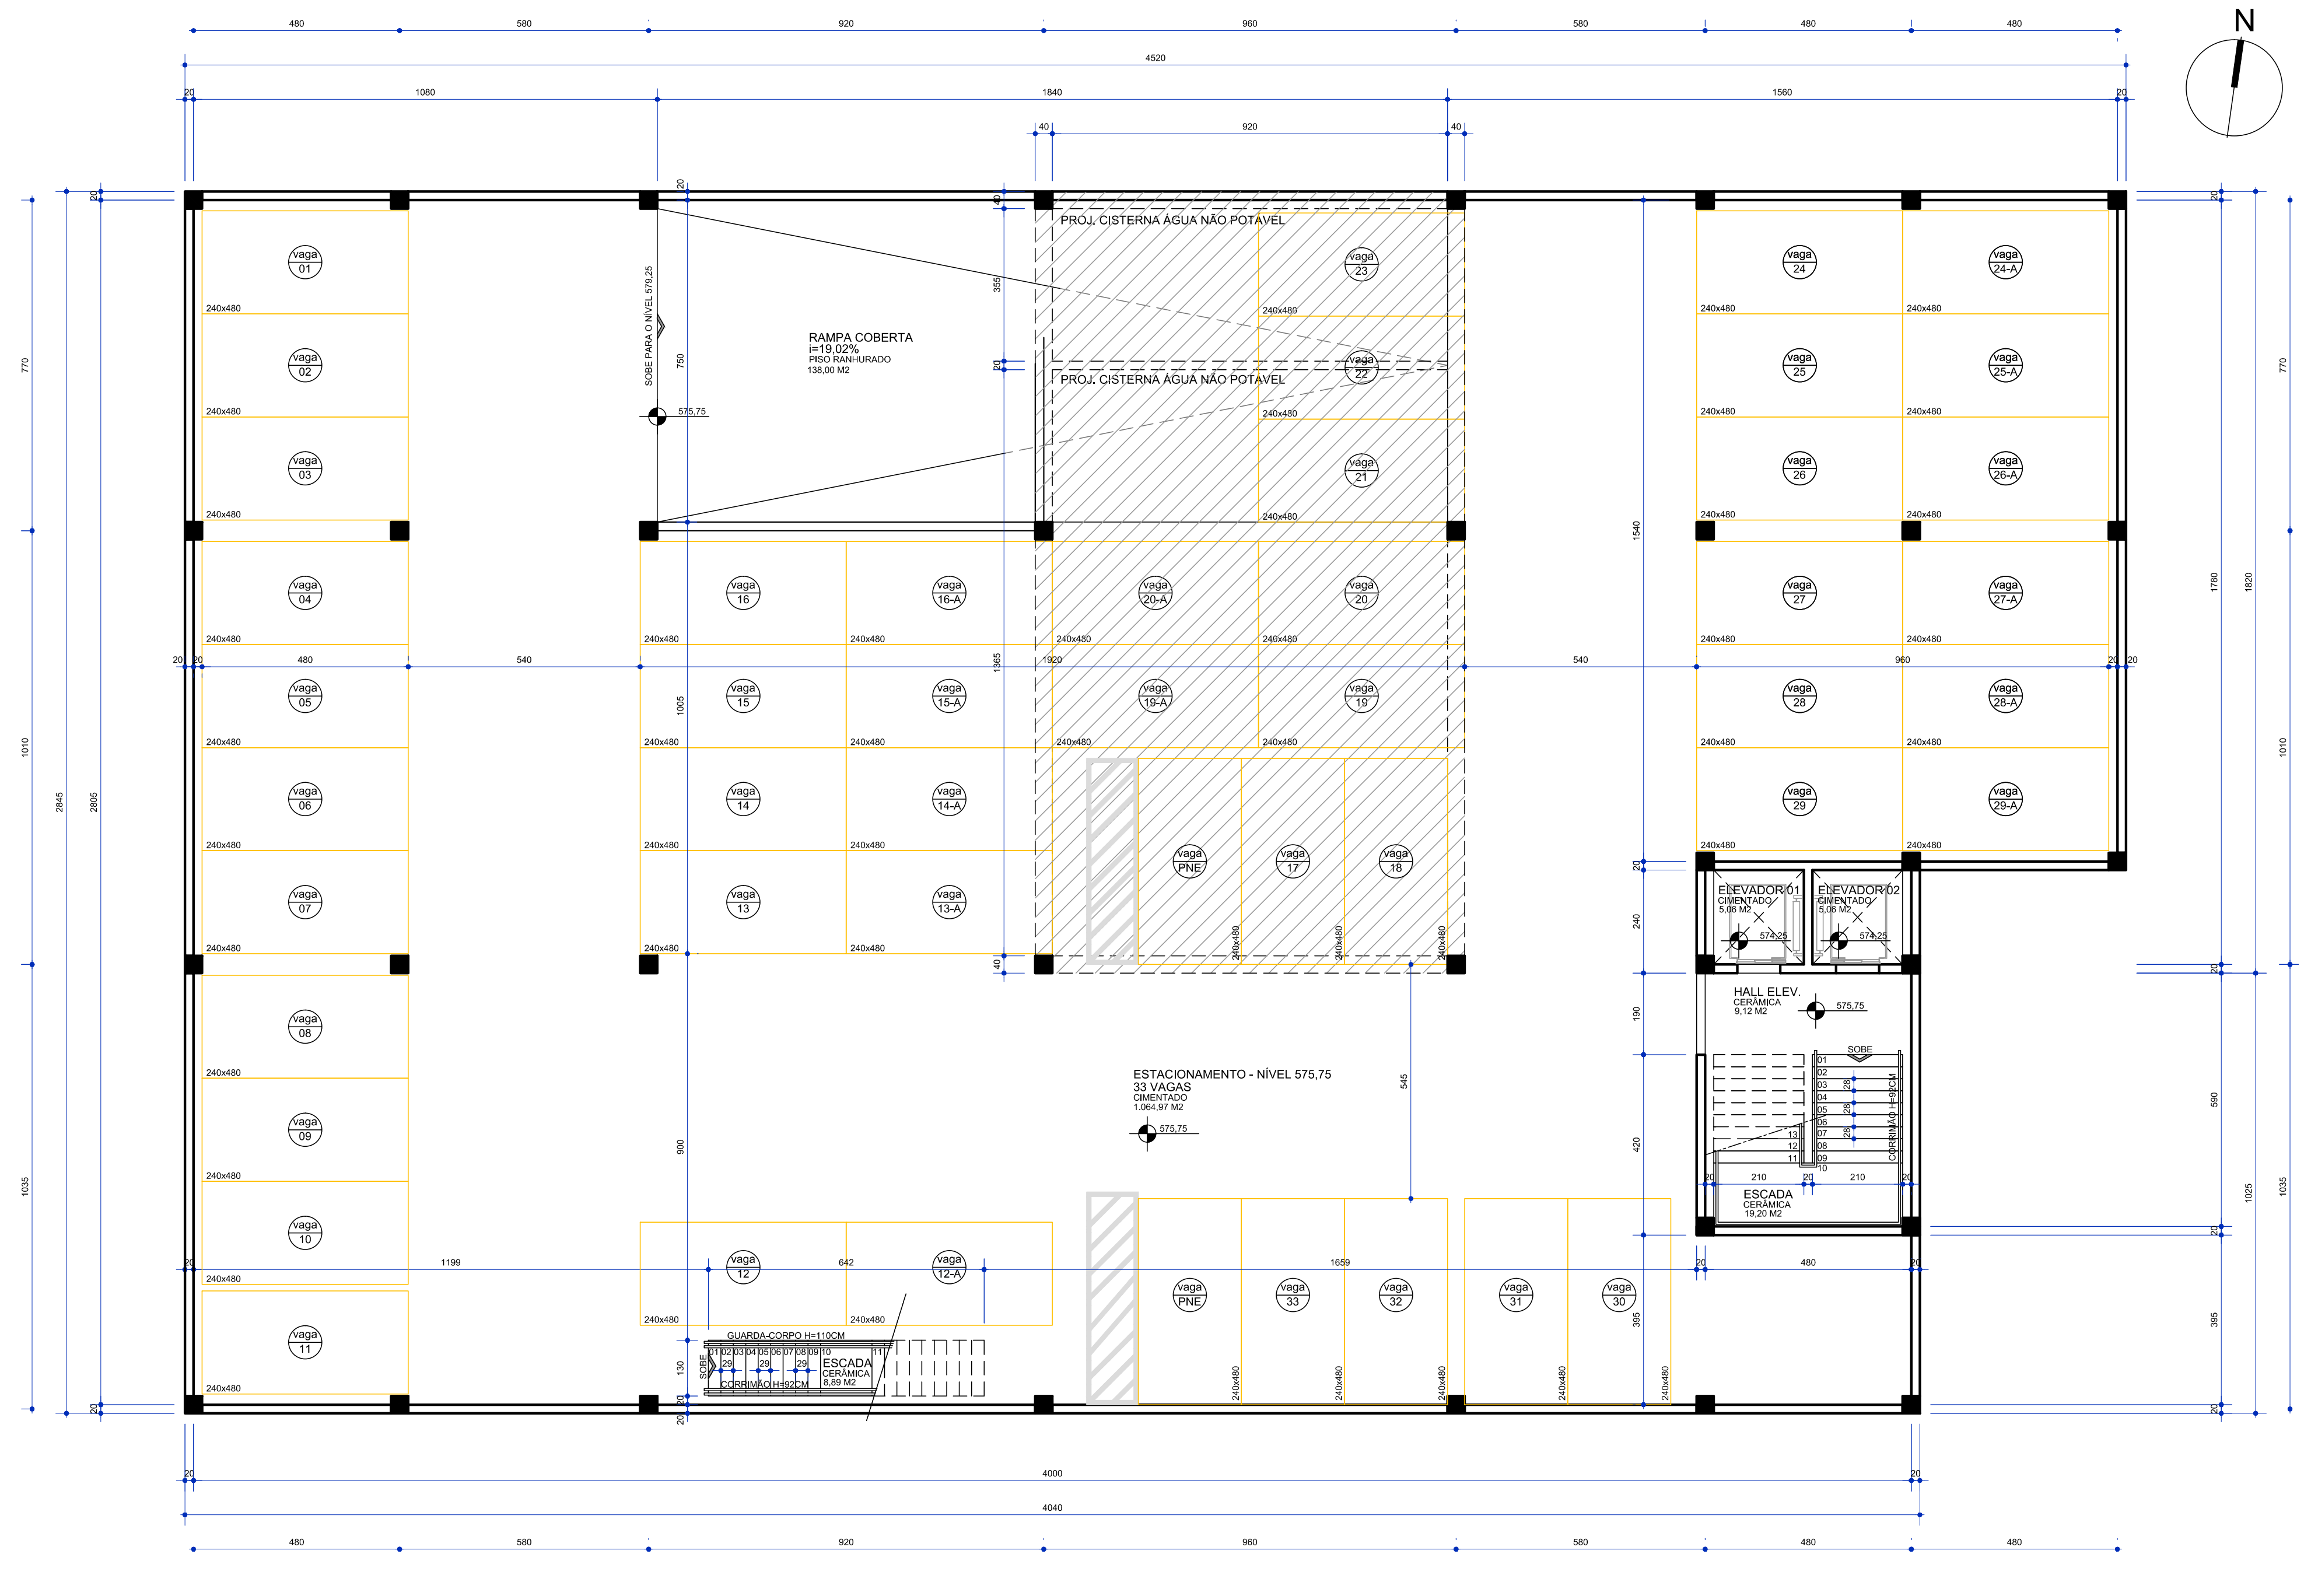

PLANTA ESTACIONAMENTO NÍVEL 575,75

ESC. 1:100

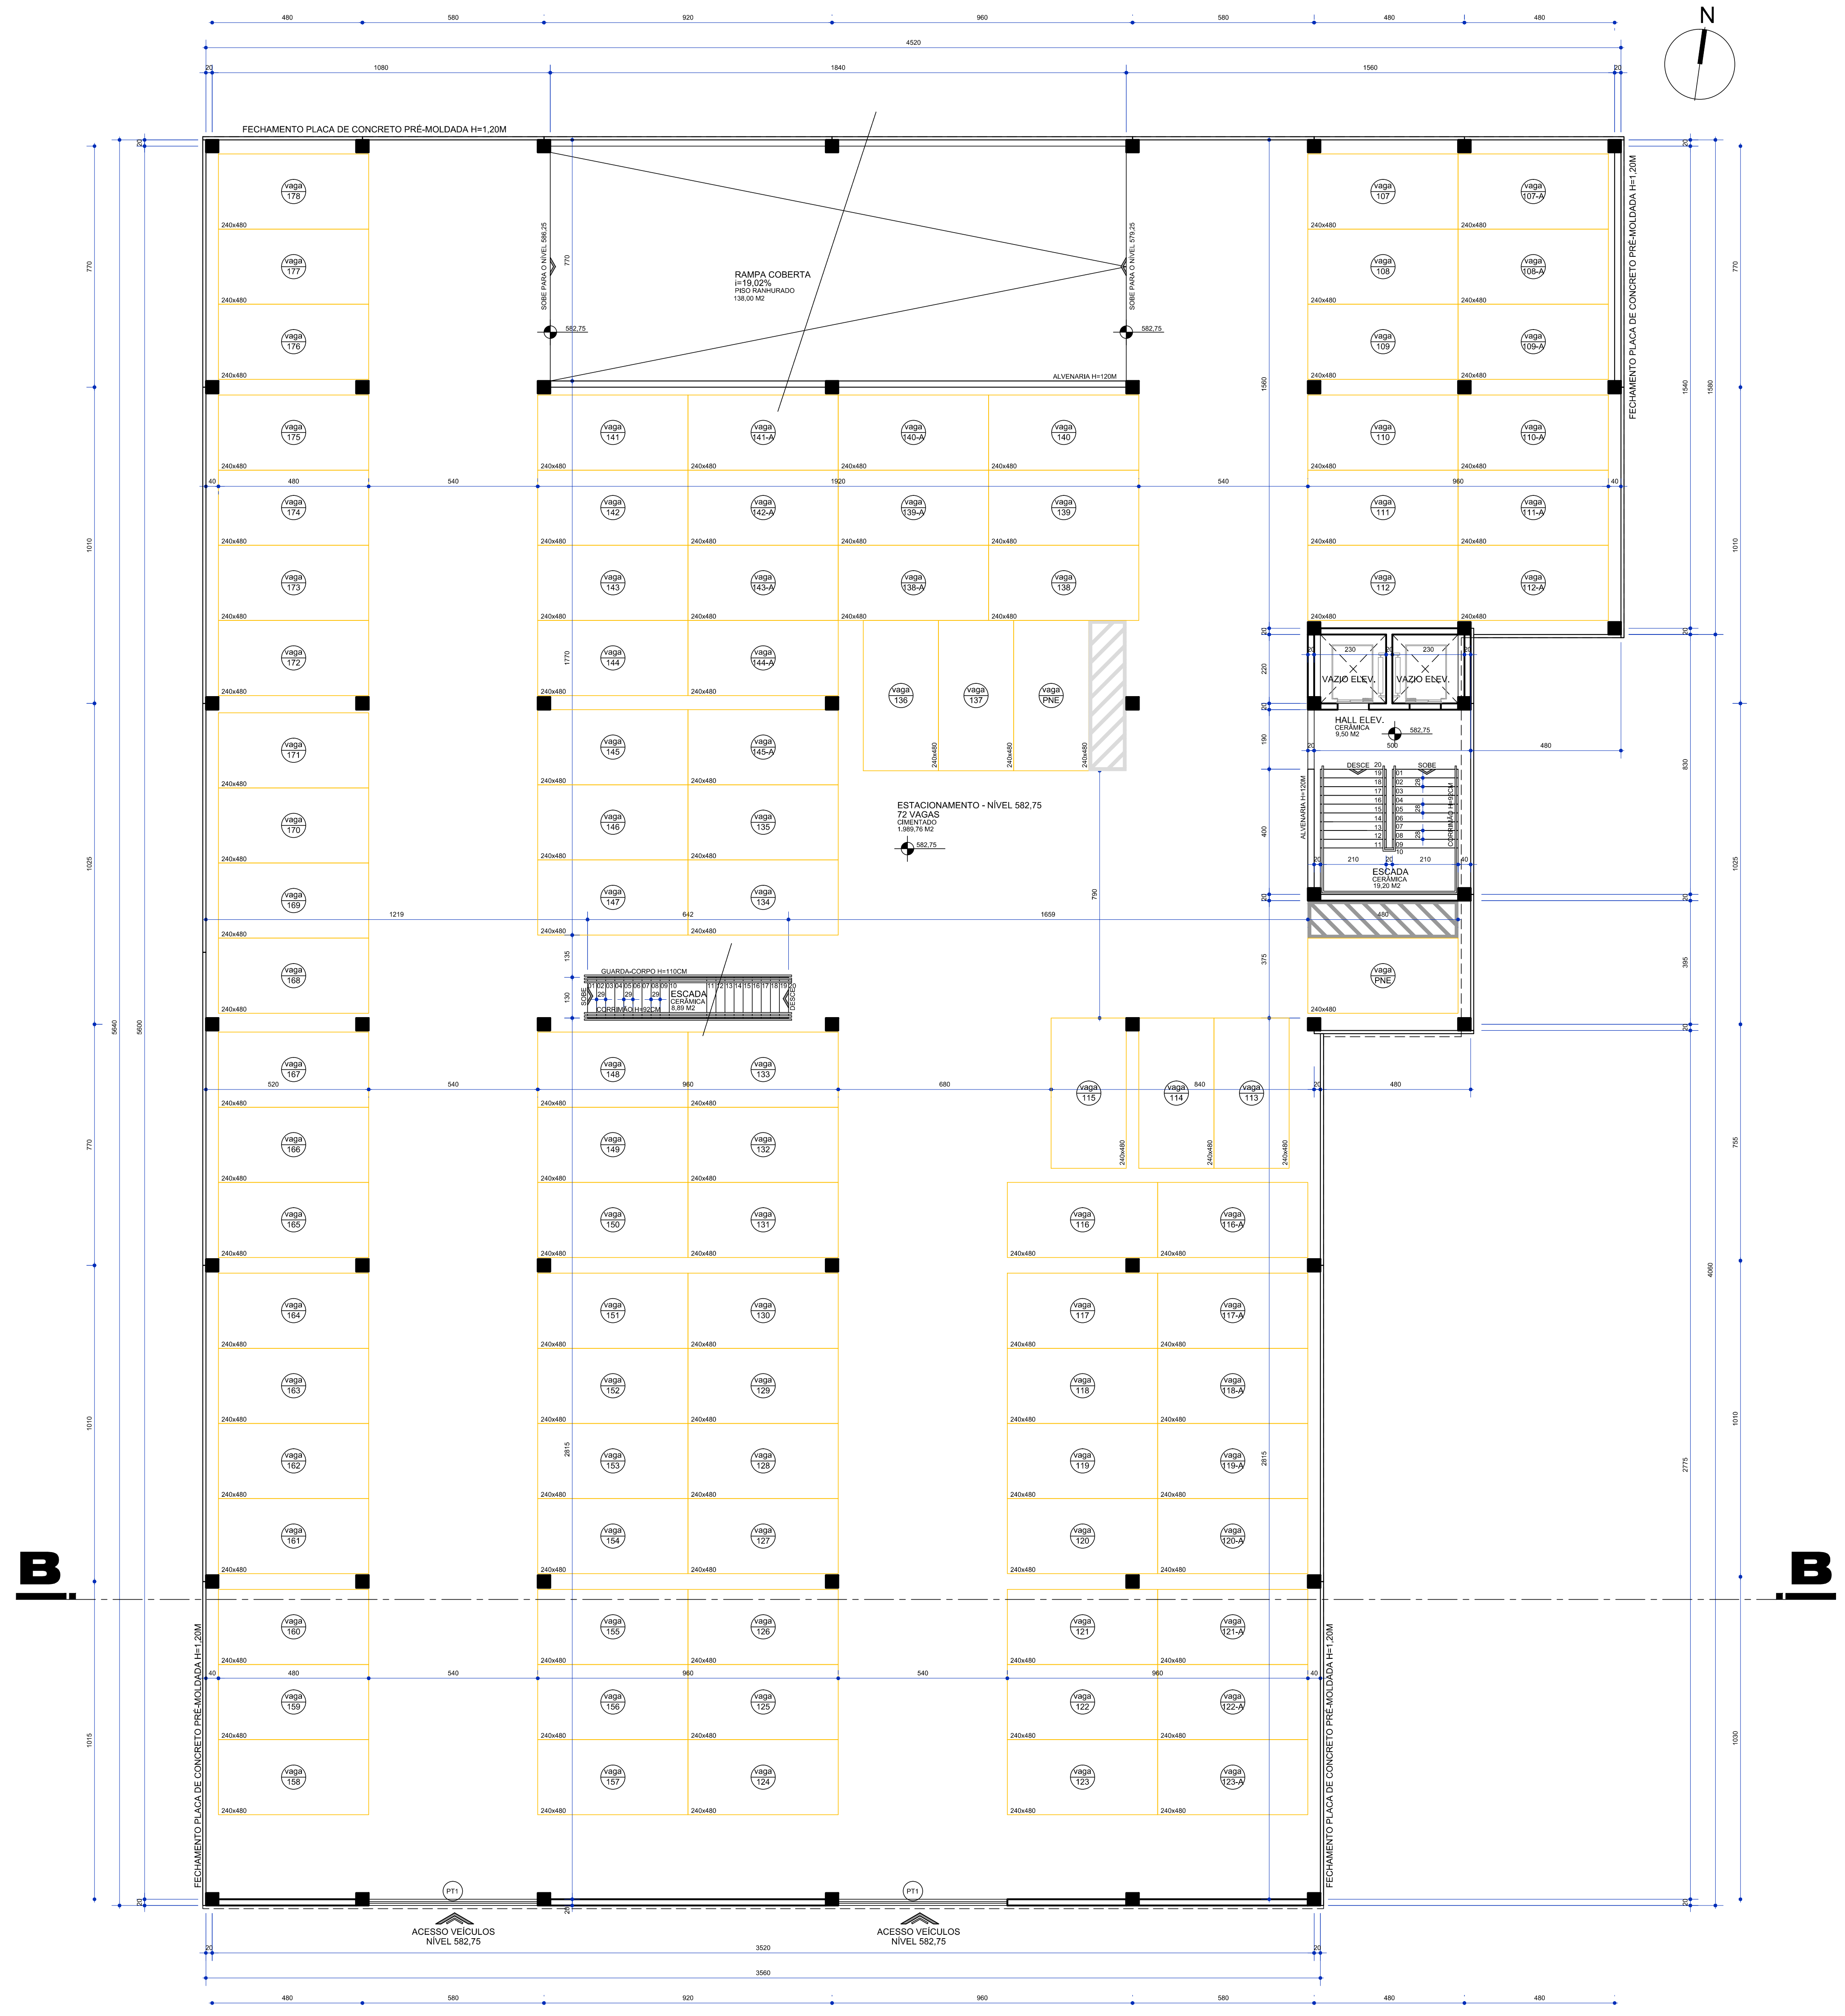

PLANTA ESTACIONAMENTO NÍVEL 582,75

ESC. 1:100

QUADRO DE ESQUADRIAS - LAZER TÉRREO

CÓD.	NOMENCL.	LARGURA	ALTURA	PEITORIL	ABERTURA	VIDRO	OBSERVAÇÕES
J01	JANELA ALUMÍNIO	120	100	120	CORRER	VD TEMP INCOLOR	ACABAMENTOS COR GRAFITE
J02	JANELA ALUMÍNIO	386	285	-	FIXO	VD TEMP INCOLOR	ACABAMENTOS COR GRAFITE
J03	JANELA ALUMÍNIO	664	285	-	CORRER/FIXO	VD TEMP INCOLOR	ACABAMENTOS COR GRAFITE
J04	JANELA FERRO	280.5	285	-	FIXO	VD TEMP INCOLOR	ACABAMENTOS COR GRAFITE
J05	JANELA ALUMÍNIO	399.5	285	-	CORRER/FIXO	VD TEMP INCOLOR	ACABAMENTOS COR GRAFITE
J06	JANELA ALUMÍNIO	688	285	-	CORRER/FIXO	VD TEMP INCOLOR	ACABAMENTOS COR GRAFITE
J07	JANELA ALUMÍNIO	300	080	205	CORRER/FIXO	VD FANTASIA	ACABAMENTOS COR GRAFITE
J08	JANELA ALUMÍNIO	120	080	205	CORRER/FIXO	VD FANTASIA	ACABAMENTOS COR GRAFITE
J09	JANELA ALUMÍNIO	180	080	205	CORRER/FIXO	VD FANTASIA	ACABAMENTOS COR GRAFITE
J10	JANELA ALUMÍNIO	360	080	205	CORRER/FIXO	VD FANTASIA	ACABAMENTOS COR GRAFITE
J11	JANELA ALUMÍNIO	660	080	205	CORRER/FIXO	VD FANTASIA	ACABAMENTOS COR GRAFITE
J12	JANELA ALUMÍNIO	672.5	285	-	FIXO	VD TEMP INCOLOR	ACABAMENTOS COR GRAFITE
J13	JANELA ALUMÍNIO	235	285	-	FIXO	VD TEMP INCOLOR	ACABAMENTOS COR GRAFITE
J14	JANELA ALUMÍNIO	215	285	-	FIXO	VD TEMP INCOLOR	ACABAMENTOS COR GRAFITE
J15	JANELA FERRO	080	050	-/150	FIXO	TELA ARTÍSTICA	ACABAMENTOS COR GRAFITE
J16	JANELA ALUMÍNIO	643	285	-	FIXO	VD TEMP INCOLOR	ACABAMENTOS COR GRAFITE
PM1	PORTA MADEIRA	080	210	-	ABRIR	-	PINTURA COR BRANCO
PM2	PORTA MADEIRA	070	210	-	ABRIR	-	PINTURA COR BRANCO
PM3	PORTA MADEIRA	060	210	-	ABRIR	-	PINTURA COR BRANCO
PM4	PORTA MADEIRA	080	210	-	ABRIR	-	COM BARRA PARA PNE
PA1	PORTA ALUMÍNIO	080	220	-	ABRIR	-	VENEZIANA ALUMÍNIO COR GRAFITE
PA2	PORTA ALUMÍNIO	070	220	-	ABRIR	-	VENEZIANA ALUMÍNIO COR GRAFITE
PA3	PORTA ALUMÍNIO	060	220	-	ABRIR	-	VENEZIANA ALUMÍNIO COR GRAFITE
PA4	PORTA ALUMÍNIO	120	220	-	ABRIR	-	VENEZIANA ALUMÍNIO COR GRAFITE
PA5	PORTA ALUMÍNIO	070	220/250	-	ABRIR	VIDRO INCOLOR	VENEZIANA ALUMÍNIO COR GRAFITE
PJ01	PORTA-JANELA	142/1170/142	350	-	ABRIR/FIXO	VD TEMP INCOLOR	ACABAMENTOS COR GRAFITE
PJ02	PORTA-JANELA	265.5	285	-	ABRIR/FIXO	VD TEMP INCOLOR	ACABAMENTOS COR GRAFITE
PJ03	PORTA-JANELA	280.5	350	-	ABRIR/FIXO	VD TEMP INCOLOR	ACABAMENTOS COR GRAFITE
PJ04	PORTA-JANELA	241.5	285	-	ABRIR/FIXO	VD TEMP INCOLOR	ACABAMENTOS COR GRAFITE
PJ05	PORTA-JANELA	360	285	-	CORRER	VD TEMP INCOLOR	ACABAMENTOS COR GRAFITE
PJ06	PORTA-JANELA	267.5	285	-	CORRER	VD TEMP INCOLOR	ACABAMENTOS COR GRAFITE
PJ07	PORTA-JANELA	180	285	-	CORRER	VD TEMP INCOLOR	ACABAMENTOS COR GRAFITE
PJ08	PORTA-JANELA	396	285	-	ABRIR/FIXO	VD TEMP INCOLOR	ACABAMENTOS COR GRAFITE
PJ09	PORTA-JANELA	150	220	-	ABRIR/FIXO	VD TEMP INCOLOR	ACABAMENTOS COR GRAFITE
PJ10	PORTA-JANELA	130	220	-	ABRIR/FIXO	VD TEMP INCOLOR	ACABAMENTOS COR GRAFITE
PJ11	PORTA-JANELA	320	285	-	CORRER	VD TEMP INCOLOR	ACABAMENTOS COR GRAFITE
PJ12	PORTA-JANELA	481	285	-	CORRER	VD TEMP INCOLOR	ACABAMENTOS COR GRAFITE
PJ13	PORTA-JANELA	400	285	-	CORRER	VD TEMP INCOLOR	ACABAMENTOS COR GRAFITE
PJ14	PORTA-JANELA	560	285	-	CORRER	VD TEMP INCOLOR	ACABAMENTOS COR GRAFITE

NOTA

O DEP. DE LIXO, DEP. GÁS E PORTARIA 02 SÃO A TÍTULO PRECÁRIO

REVISÕES

DATA	PROCEDIMENTO
24/07/2023	ENTREGA-R00
24/08/2023	ENTREGA-R01
13/09/2023	ENTREGA-R02

MIGUEL VIANI	ARQUITETO E URBANISTA - CAU A126752-3
VITOR GIROLDO	ARQUITETO E URBANISTA - CAU A63642-8
RENATO VIANI	ARQUITETO E URBANISTA - CAU A30683-5

viani
ARQUITETURA
rua joão wyclif 111 sl 107 : 86050-450 palhano : londrina-pr : [43]3028-3990 : contato@vianiarquitetura.com.br
www.vianiarquitetura.com.br

YTICON CONSTRUÇÃO E INCORPORAÇÃO LTDA.
13 SETEMBRO 2023
LONDRINA-PR
ESTAC_575,75_582,75-PREF-R02.dwg
391

TÍTULO DA PRANCHA PROJETO ARQUITETÔNICO PLANTA ESTACIONAMENTO NÍVEL 575,75 E NÍVEL 582,75	PRANCHA PL02 /12	ESCALA INDICADAS
USO DA EDIFICAÇÃO CONSTRUÇÃO DE: EDIFICAÇÃO RESIDENCIAL MULTIFAMILIAR VERTICAL [RMV]	ZONEAMENTO ZR7	COEF. DE APROVEITAMENTO 2,91 (MÁX:3,50)
LOCAL DA OBRA LOTE 101/A, DA SUBDIVISÃO DO LOTE 101 REMANESCENTE, SITUADO NO RIBEIRÃO DA ESPERANÇA, FAZENDA PALHANO, LONDRINA-PR	DATA DO PROJETO 24/07/2023	TAXA DE OCUPAÇÃO 61,77% (MÁX: 80%)
PROPRIETÁRIO YTICON CONSTRUÇÃO E INCORPORAÇÃO LTDA	CNPJ 10.910.748/0001-85 INSCRIÇÃO IMOBILIÁRIA 06020259103960001	

SITUAÇÃO SEM ESCALA

QUADRO DE ÁREAS - VER PRANCHA PL05

DECLARO QUE A APROVAÇÃO DO PROJETO NÃO IMPLICA NO RECONHECIMENTO POR PARTE DA PREFEITURA DO DIREITO DE PROPRIEDADE DO TERRENO.

BRUNO RAFAEL CATARINO:04244617906
Assinado de forma digital por BRUNO RAFAEL CATARINO:04244617906
Dados: 2023.09.13 17:36:40 -03'00'

PROPRIETÁRIO
YTICON CONSTRUÇÃO E INCORPORAÇÃO LTDA.
CNPJ 10.910.748/0001-85

RENATO MATEUS GORNE VIANI:02635778990
Assinado de forma digital por RENATO MATEUS GORNE VIANI:02635778990
Dados: 2023.09.13 16:50:24 -03'00'

AUTOR DO PROJETO
RENATO MATEUS GORNE VIANI
ARQUITETO E URBANISTA - CAU A30683-9

IVANI GONCALVES DA SILVA MARIANO:67369553949
Assinado de forma digital por IVANI GONCALVES DA SILVA MARIANO:67369553949
Dados: 2023.09.14 09:06:49 -03'00'

RESPONSÁVEL TÉCNICO PELA EXECUÇÃO DA OBRA
IVANI GONÇALVES DA SILVA MARIANO
ENGENHEIRA CIVIL - CREA PR-27711/D

Assinatura Eletrônica

DIRETORIA APROVAÇÃO DE PROJETOS
Londrina, 22 de setembro de 2023.
Processo Aprovação nº 19.021.125875/2023-06
Nº de ORDEM: 2457/2023
Nº de ALVARÁ: 2457/2023

MARCELO PAGOTTO CARNEIRO
Matrícula nº 13577-1

ESPAÇO RESERVADO PARA APROVAÇÃO (Observações):

MARCELO PAGOTTO CARNEIRO:01643439979
Assinado de forma digital por MARCELO PAGOTTO CARNEIRO:01643439979
Dados: 2023.09.27 13:16:46 -03'00'