


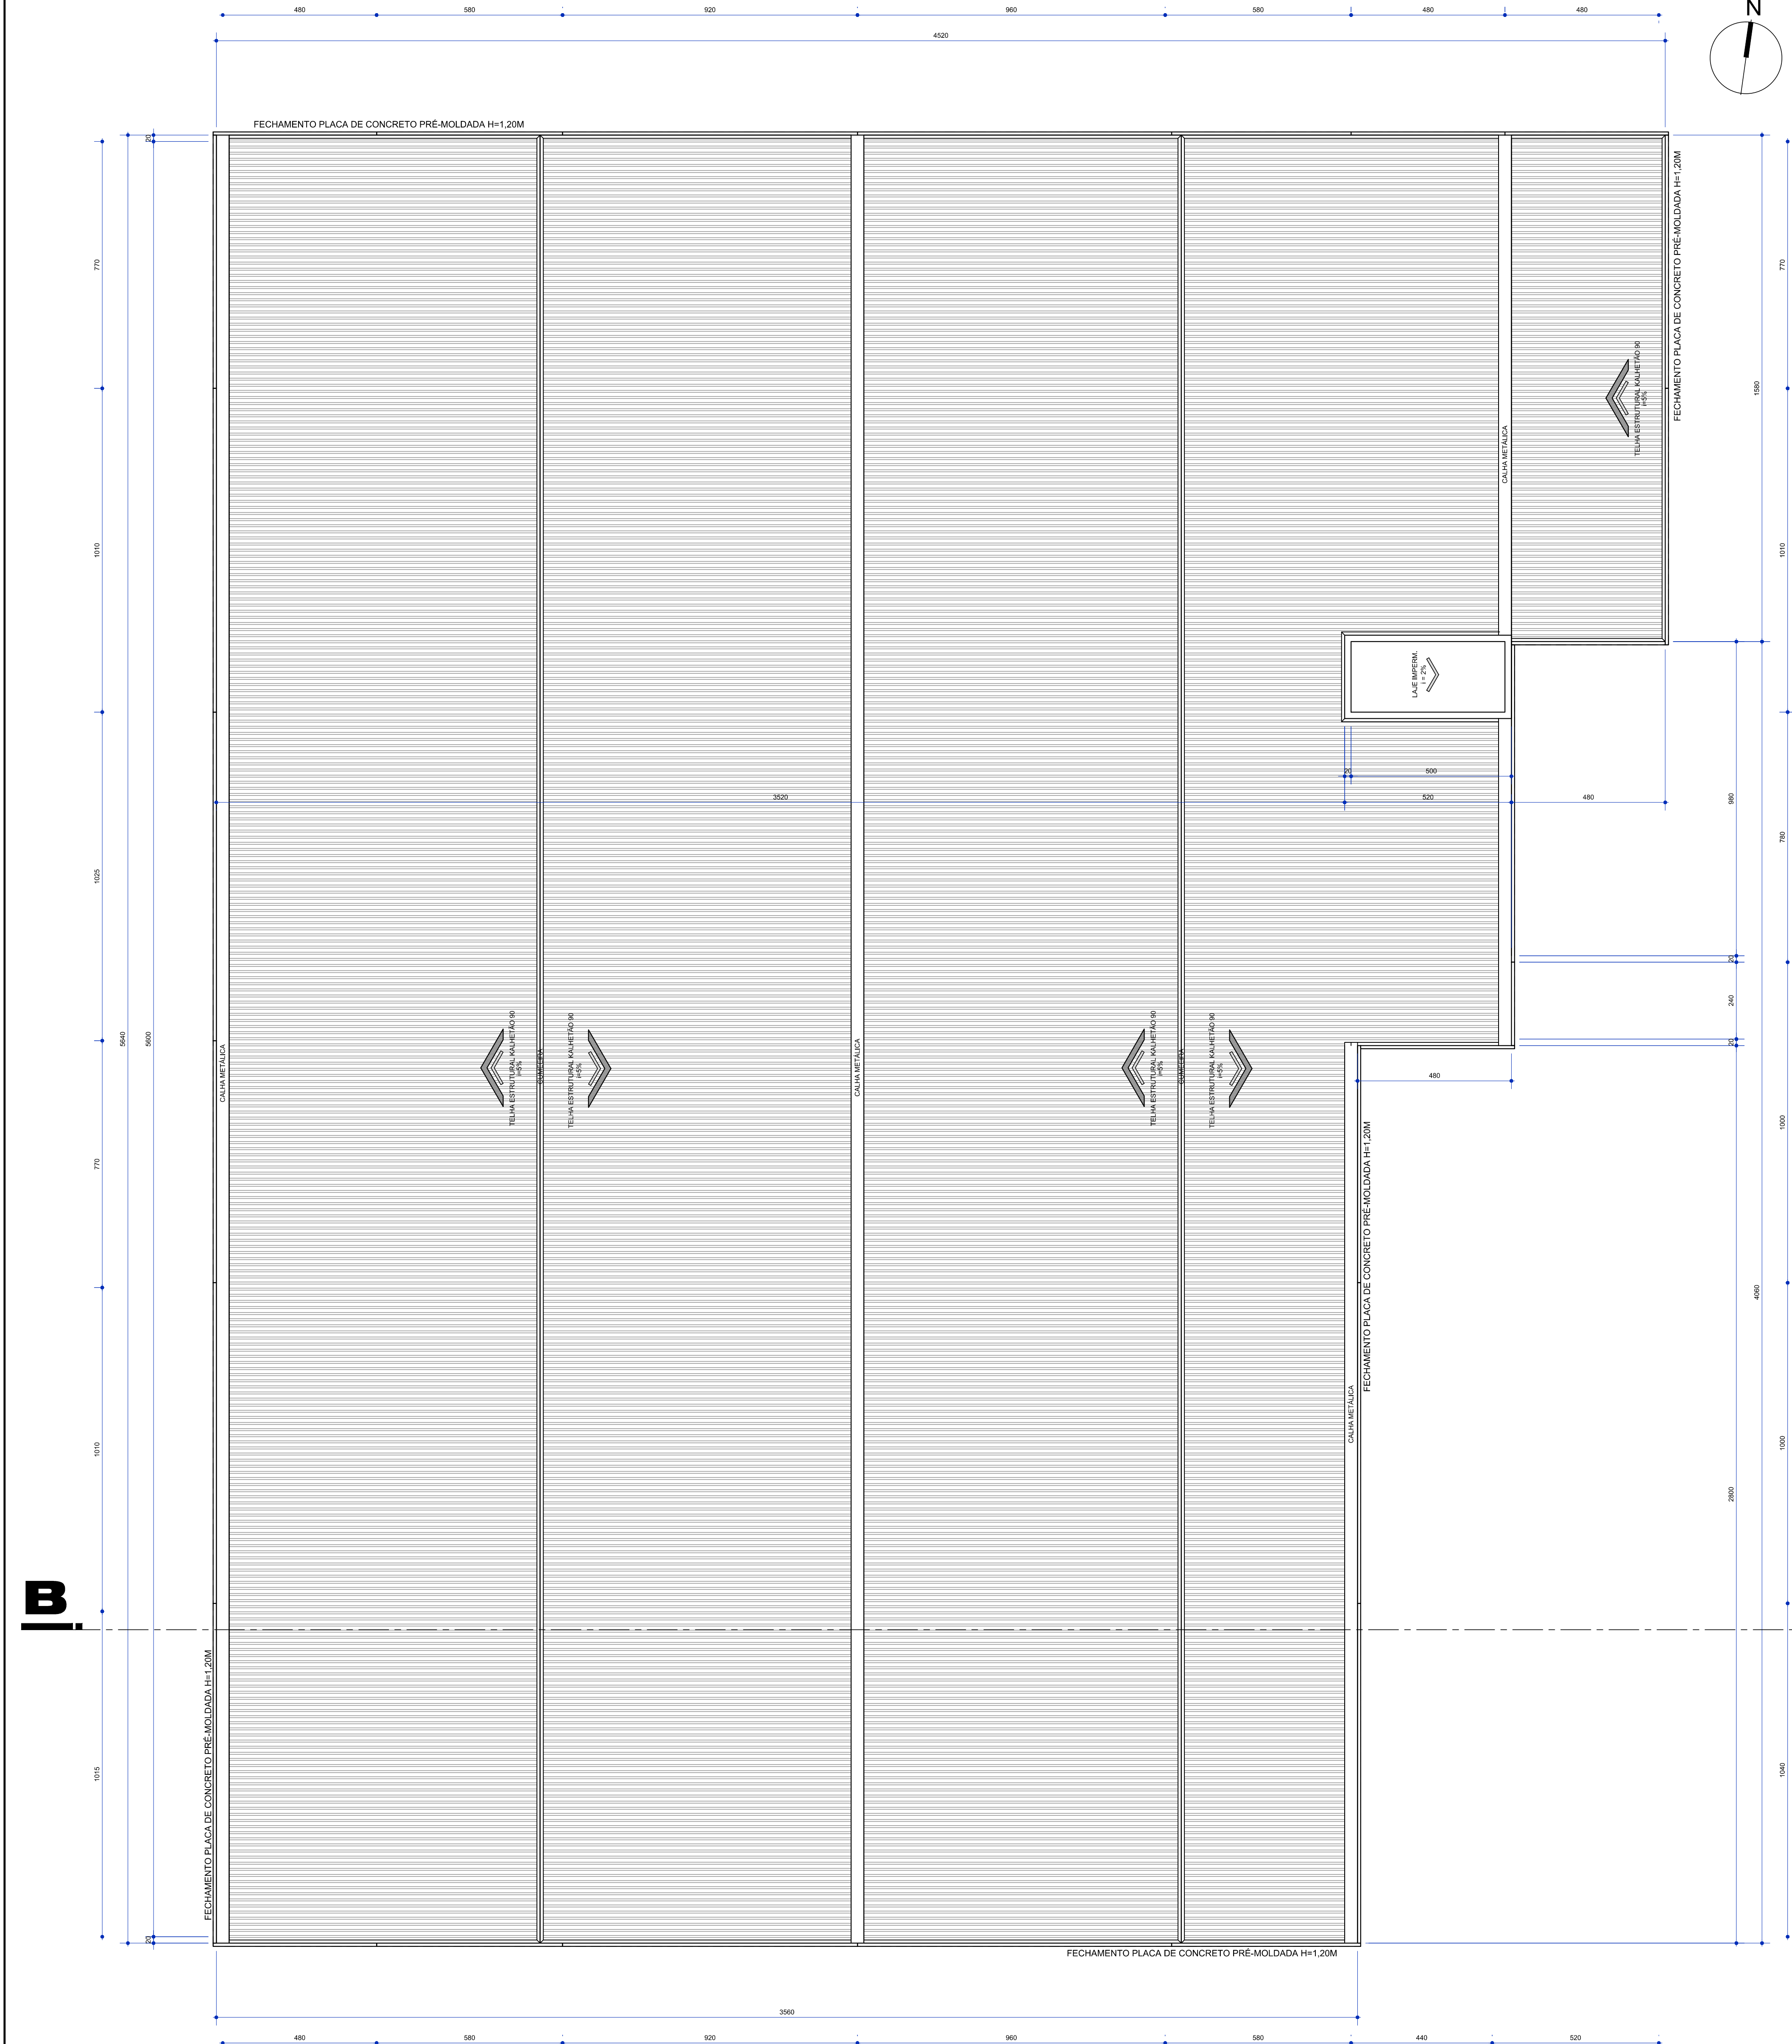

PLANTA COBERTURA ESTACIONAMENTO

ESC. 1:100

QUADRO DE ESQUADRIAS - LAZER TÉRREO

CÓD.	NOMENCL.	LARGURA	ALTURA	PEITORIL	ABERTURA	VIDRO	OBSERVAÇÕES
J01	JANELA ALUMÍNIO	120	100	120	CORRER	VD TEMP INCOLOR	ACABAMENTOS COR GRAFITE
J02	JANELA ALUMÍNIO	388	285	-	FIXO	VD TEMP INCOLOR	ACABAMENTOS COR GRAFITE
J03	JANELA ALUMÍNIO	684	285	-	CORRER/FIXO	VD TEMP INCOLOR	ACABAMENTOS COR GRAFITE
J04	JANELA FERRO	290,5	285	-	FIXO	VD TEMP INCOLOR	ACABAMENTOS COR GRAFITE
J05	JANELA ALUMÍNIO	399,5	285	-	CORRER/FIXO	VD TEMP INCOLOR	ACABAMENTOS COR GRAFITE
J06	JANELA ALUMÍNIO	688	285	-	CORRER/FIXO	VD TEMP INCOLOR	ACABAMENTOS COR GRAFITE
J07	JANELA ALUMÍNIO	300	080	205	CORRER/FIXO	VD FANTASIA	ACABAMENTOS COR GRAFITE
J08	JANELA ALUMÍNIO	120	080	205	CORRER/FIXO	VD FANTASIA	ACABAMENTOS COR GRAFITE
J09	JANELA ALUMÍNIO	180	080	205	CORRER/FIXO	VD FANTASIA	ACABAMENTOS COR GRAFITE
J10	JANELA ALUMÍNIO	360	080	205	CORRER/FIXO	VD FANTASIA	ACABAMENTOS COR GRAFITE
J11	JANELA ALUMÍNIO	660	080	205	CORRER/FIXO	VD FANTASIA	ACABAMENTOS COR GRAFITE
J12	JANELA ALUMÍNIO	672,5	285	-	FIXO	VD TEMP INCOLOR	ACABAMENTOS COR GRAFITE
J13	JANELA ALUMÍNIO	235	285	-	FIXO	VD TEMP INCOLOR	ACABAMENTOS COR GRAFITE
J14	JANELA ALUMÍNIO	215	285	-	FIXO	VD TEMP INCOLOR	ACABAMENTOS COR GRAFITE
J15	JANELA FERRO	080	050	-150	FIXO	TELA ARTISTICA	ACABAMENTOS COR GRAFITE
J16	JANELA ALUMÍNIO	643	285	-	FIXO	VD TEMP INCOLOR	ACABAMENTOS COR GRAFITE

PM1	PORTA MADEIRA	080	210	-	ABRIR	-	PINTURA COR BRANCO
PM2	PORTA MADEIRA	070	210	-	ABRIR	-	PINTURA COR BRANCO
PM3	PORTA MADEIRA	060	210	-	ABRIR	-	PINTURA COR BRANCO
PM4	PORTA MADEIRA	090	210	-	ABRIR	-	COM BARRA PARA PNE
PA1	PORTA ALUMÍNIO	080	220	-	ABRIR	-	VENEZIANA ALUMÍNIO COR GRAFITE
PA2	PORTA ALUMÍNIO	070	220	-	ABRIR	-	VENEZIANA ALUMÍNIO COR GRAFITE
PA3	PORTA ALUMÍNIO	060	220	-	ABRIR	-	VENEZIANA ALUMÍNIO COR GRAFITE
PA4	PORTA ALUMÍNIO	120	220	-	ABRIR	-	VENEZIANA ALUMÍNIO COR GRAFITE
PA5	PORTA ALUMÍNIO	070	220/250	-	ABRIR	VIDRO INCOLOR	VENEZIANA ALUMÍNIO COR GRAFITE

PJ01	PORTA-JANELA	142/1170/142	350	-	ABRIR/FIXO	VD TEMP INCOLOR	ACABAMENTOS COR GRAFITE
PJ02	PORTA-JANELA	265,5	285	-	ABRIR/FIXO	VD TEMP INCOLOR	ACABAMENTOS COR GRAFITE
PJ03	PORTA-JANELA	280,5	350	-	ABRIR/FIXO	VD TEMP INCOLOR	ACABAMENTOS COR GRAFITE
PJ04	PORTA-JANELA	241,5	285	-	ABRIR/FIXO	VD TEMP INCOLOR	ACABAMENTOS COR GRAFITE
PJ05	PORTA-JANELA	360	285	-	CORRER	VD TEMP INCOLOR	ACABAMENTOS COR GRAFITE
PJ06	PORTA-JANELA	287,5	285	-	CORRER	VD TEMP INCOLOR	ACABAMENTOS COR GRAFITE
PJ07	PORTA-JANELA	180	285	-	CORRER	VD TEMP INCOLOR	ACABAMENTOS COR GRAFITE
PJ08	PORTA-JANELA	395	285	-	ABRIR/FIXO	VD TEMP INCOLOR	ACABAMENTOS COR GRAFITE
PJ09	PORTA-JANELA	150	220	-	ABRIR/FIXO	VD TEMP INCOLOR	ACABAMENTOS COR GRAFITE
PJ10	PORTA-JANELA	130	220	-	ABRIR/FIXO	VD TEMP INCOLOR	ACABAMENTOS COR GRAFITE
PJ11	PORTA-JANELA	400	285	-	CORRER	VD TEMP INCOLOR	ACABAMENTOS COR GRAFITE
PJ12	PORTA-JANELA	451	285	-	CORRER	VD TEMP INCOLOR	ACABAMENTOS COR GRAFITE
PJ13	PORTA-JANELA	400	285	-	CORRER	VD TEMP INCOLOR	ACABAMENTOS COR GRAFITE
PJ14	PORTA-JANELA	560	285	-	CORRER	VD TEMP INCOLOR	ACABAMENTOS COR GRAFITE

NOTA

O DEP. DE LIXO, DEP. GÁS E PORTARIA 02 SÃO A TÍTULO PRECÁRIO

REVISÕES

DATA PROCEDIMENTO

24/07/2023	ENTREGA-R00
24/08/2023	ENTREGA-R01

MIGUEL VIANI
VITOR BRODLO
RENATO VIANI
rui jobo wyolf 1111 sl 107 - 86050-450 palhano - londrina-pr - [43]3029-3990 - contato@vianiarquitetura.com.br
www.vianiarquitetura.com.br

ARQUITETO E URBANISTA - CAU A120752-3
ARQUITETO E URBANISTA - CAU A04042-4
ARQUITETO E URBANISTA - CAU A30053-1

viani
ARQUITETURA

YTICON CONSTRUÇÃO E INCORPORAÇÃO LTDA. ESTAC_COBERTURA-PREF-R00.dwg

391

TÍTULO DA PRANCHA PROJETO ARQUITETÔNICO		PRANCHA PL04 /12	ESCALA INDICADAS
PLANTA COBERTURA ESTACIONAMENTO		ZONEAMENTO ZR7	COEF. DE APROVEITAMENTO 2,91 (MÁX: 3,50)
USO DA EDIFICAÇÃO CONSTRUÇÃO DE: EDIFICAÇÃO RESIDENCIAL MULTIFAMILIAR VERTICAL [RMV]		DATA DO PROJETO 24/07/2023	TAXA DE OCUPAÇÃO 61,77% (MÁX: 80%)
LOCAL DA OBRA LOTE 101/A, DA SUBDIVISÃO DO LOTE 101 REMANESCENTE, SITUADO NO RIBEIRÃO DA ESPERANÇA, FAZENDA PALHANO, LONDRIANA-PR		PROPRIETÁRIO YTICON CONSTRUÇÃO E INCORPORAÇÃO LTDA	CNPJ 10.910.748/0001-85 INSCRIÇÃO IMOBILIÁRIA 06020259103960001
SITUAÇÃO SEM ESCALA		DECLARO QUE A APROVAÇÃO DO PROJETO NÃO IMPLICA NO RECONHECIMENTO POR PARTE DA PREFEITURA DO DIREITO DE PROPRIEDADE DO TERRENO.	
QUADRO DE ÁREAS - VER PRANCHA PLO5		BRUNO RAFAEL CATARIN O:042446 17906 Assinado de forma digital por BRUNO RAFAEL CATARIN O:042446 Data: 2023.09.25 16:23:34 -03'00'	
		PROPRIETÁRIO YTICON CONSTRUÇÃO E INCORPORAÇÃO LTDA. CNPJ 10.910.748/0001-85	
		RENATO MATEUS GORNE VIANI:0263577899 0 Assinado de forma digital por RENATO MATEUS GORNE VIANI:0263577899 Data: 2023.08.24 11:16:29 -03'00'	
		AUTOR DO PROJETO RENATO MATEUS GORNE VIANI ARQUITETO E URBANISTA - CAU A30683-0	
		IVANI GONCALVES DA SILVA MARIANO:673695539 49 Assinado de forma digital por IVANI GONCALVES DA SILVA MARIANO:673695539 Data: 2023.09.25 17:02:51 -03'00'	
		RESPONSÁVEL TÉCNICO PELA EXECUÇÃO DA OBRA IVANI GONCALVES DA SILVA MARIANO ENGENHEIRA CIVIL - CREA PR-27711/D	
Assinatura Eletrônica		ESPAÇO RESERVADO PARA APROVAÇÃO (Observações):	
DIRETORIA APROVAÇÃO DE PROJETOS Londrina, 22 de setembro de 2023. Processo Aprovação nº 19.021.125878/2023-06 Nº de ORDEM: 2457/2023 Nº de ALVARÁ: 2457/2023 MARCELO PAGOTTO CARNEIRO Matricula nº 13577-1			