

CÁLCULO ÁREA DE LAZER MÍNIMA	
(1º AO 20º) PAV. TIPO - 66,02 X 160 APTOS	10.563,20
(1º AO 20º) PAV. TIPO - 65,985 X 80 APTOS	5.278,80
(1º AO 20º) PAV. TIPO - 55,00 X 80 APTOS	4.400,00
ÁREA PRIVATIVA COMPUTÁVEL TOTAL	20.242,00
Am = ÁREA MÍNIMA = 10% DA ÁREA COMPUTÁVEL	2.024,20
ÁREA DE LAZER COBERTA DO PROJETO	1.275,94
ÁREA DE LAZER DESCOBERTA DO PROJETO	1.989,19
ÁREA DE LAZER TOTAL	3.265,13


LEGENDA:

- ÁREA DE LAZER COBERTA PAV. TÉRREO = 1.275,94m2
- ÁREA DE LAZER DESCOBERTA PAV. TÉRREO = 1.989,19m2



PAV. NÍVEL 579,25 [TÉRREO]

TOTAL TERREO COBERTO: (ÁREA PARA CÁLCULO DE TAXA DE OCUPAÇÃO) TOTAL	4.211,29 m2
DESCOBERTAS:	
CIRCULAÇÃO GARAGEM	58,69 m2
CIRCULAÇÃO PEDESTRES	933,60 m2
QUADRAS	347,95 m2
PISCINAS	87,70 m2
TOTAL	1.427,94 m2
TOTAL PAV. NÍVEL 579,25 (TÉRREO) (COBERTO+DESCOBERTO)	5.639,23 m2

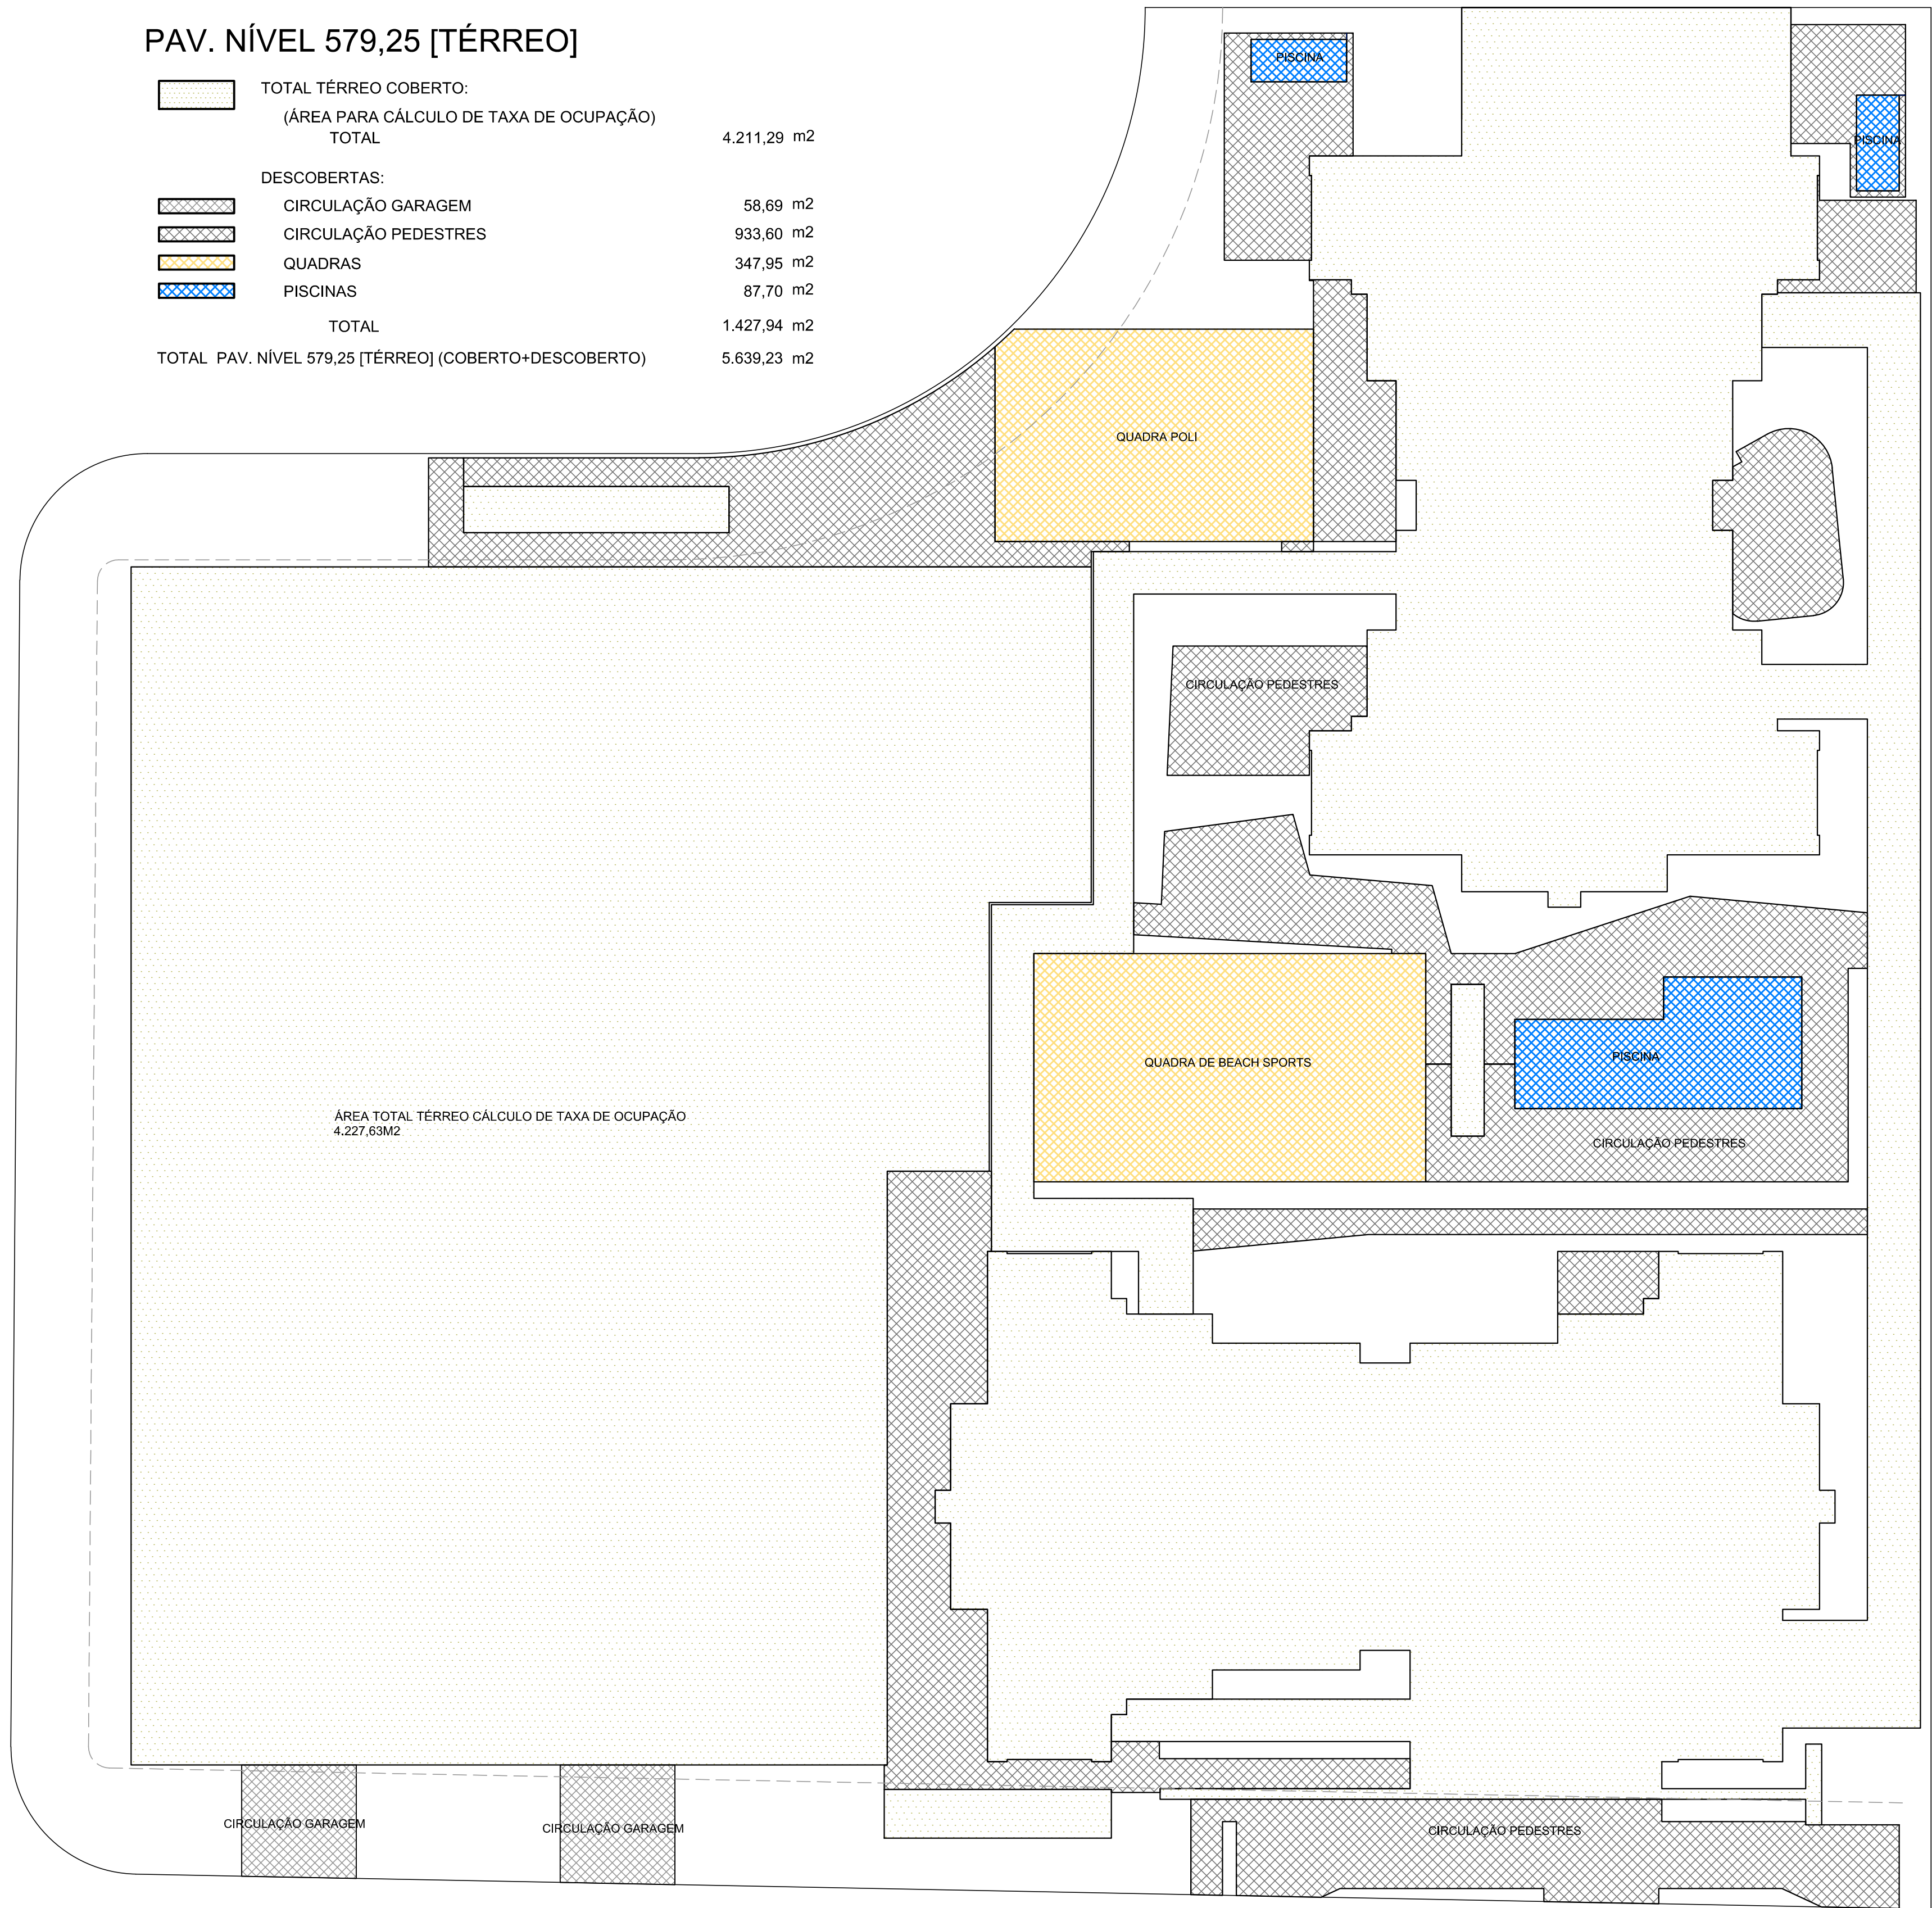

MEMORIAL CÁLCULO DE ÁREA - ÁREAS COBERTAS E DESCOBERTAS TÉRREO (NÍVEL 579,25)

ESC: 1:200

CÁLCULO TAXA DE PERMEABILIDADE


LEGENDA:

ÁREA PERMEÁVEL GRAMA 1343,20M2	
ÁREA PERMEÁVEL AREIA 189,67M2	
AP01 361,65 m2	AP02 52,62 m2
AP03 52,17 m2	AP04 92,52 m2
AP05 7,19 m2	AP06 1,74 m2
AP07 12,40 m2	AP08 33,00 m2
AP09 2,18 m2	AP10 5,28 m2
AP11 11,18 m2	AP12 68,59 m2
AP13 161,57 m2	AP14 61,34 m2
AP15 6,78 m2	AP16 164,57 m2
AP17 4,84 m2	AP18 2,62 m2
AP19 3,18 m2	AP20 65,50 m2
AP21 3,00 m2	AP22 38,81 m2
AP23 98,17 m2	AP24 7,84 m2
AP25 4,46 m2	AP26 189,67 m2

TOTAL ÁREA PERMEÁVEL: 1.532,87 M2

MEMORIAL CÁLCULO DE ÁREA - ÁREA PERMEÁVEL

ESC: 1:200

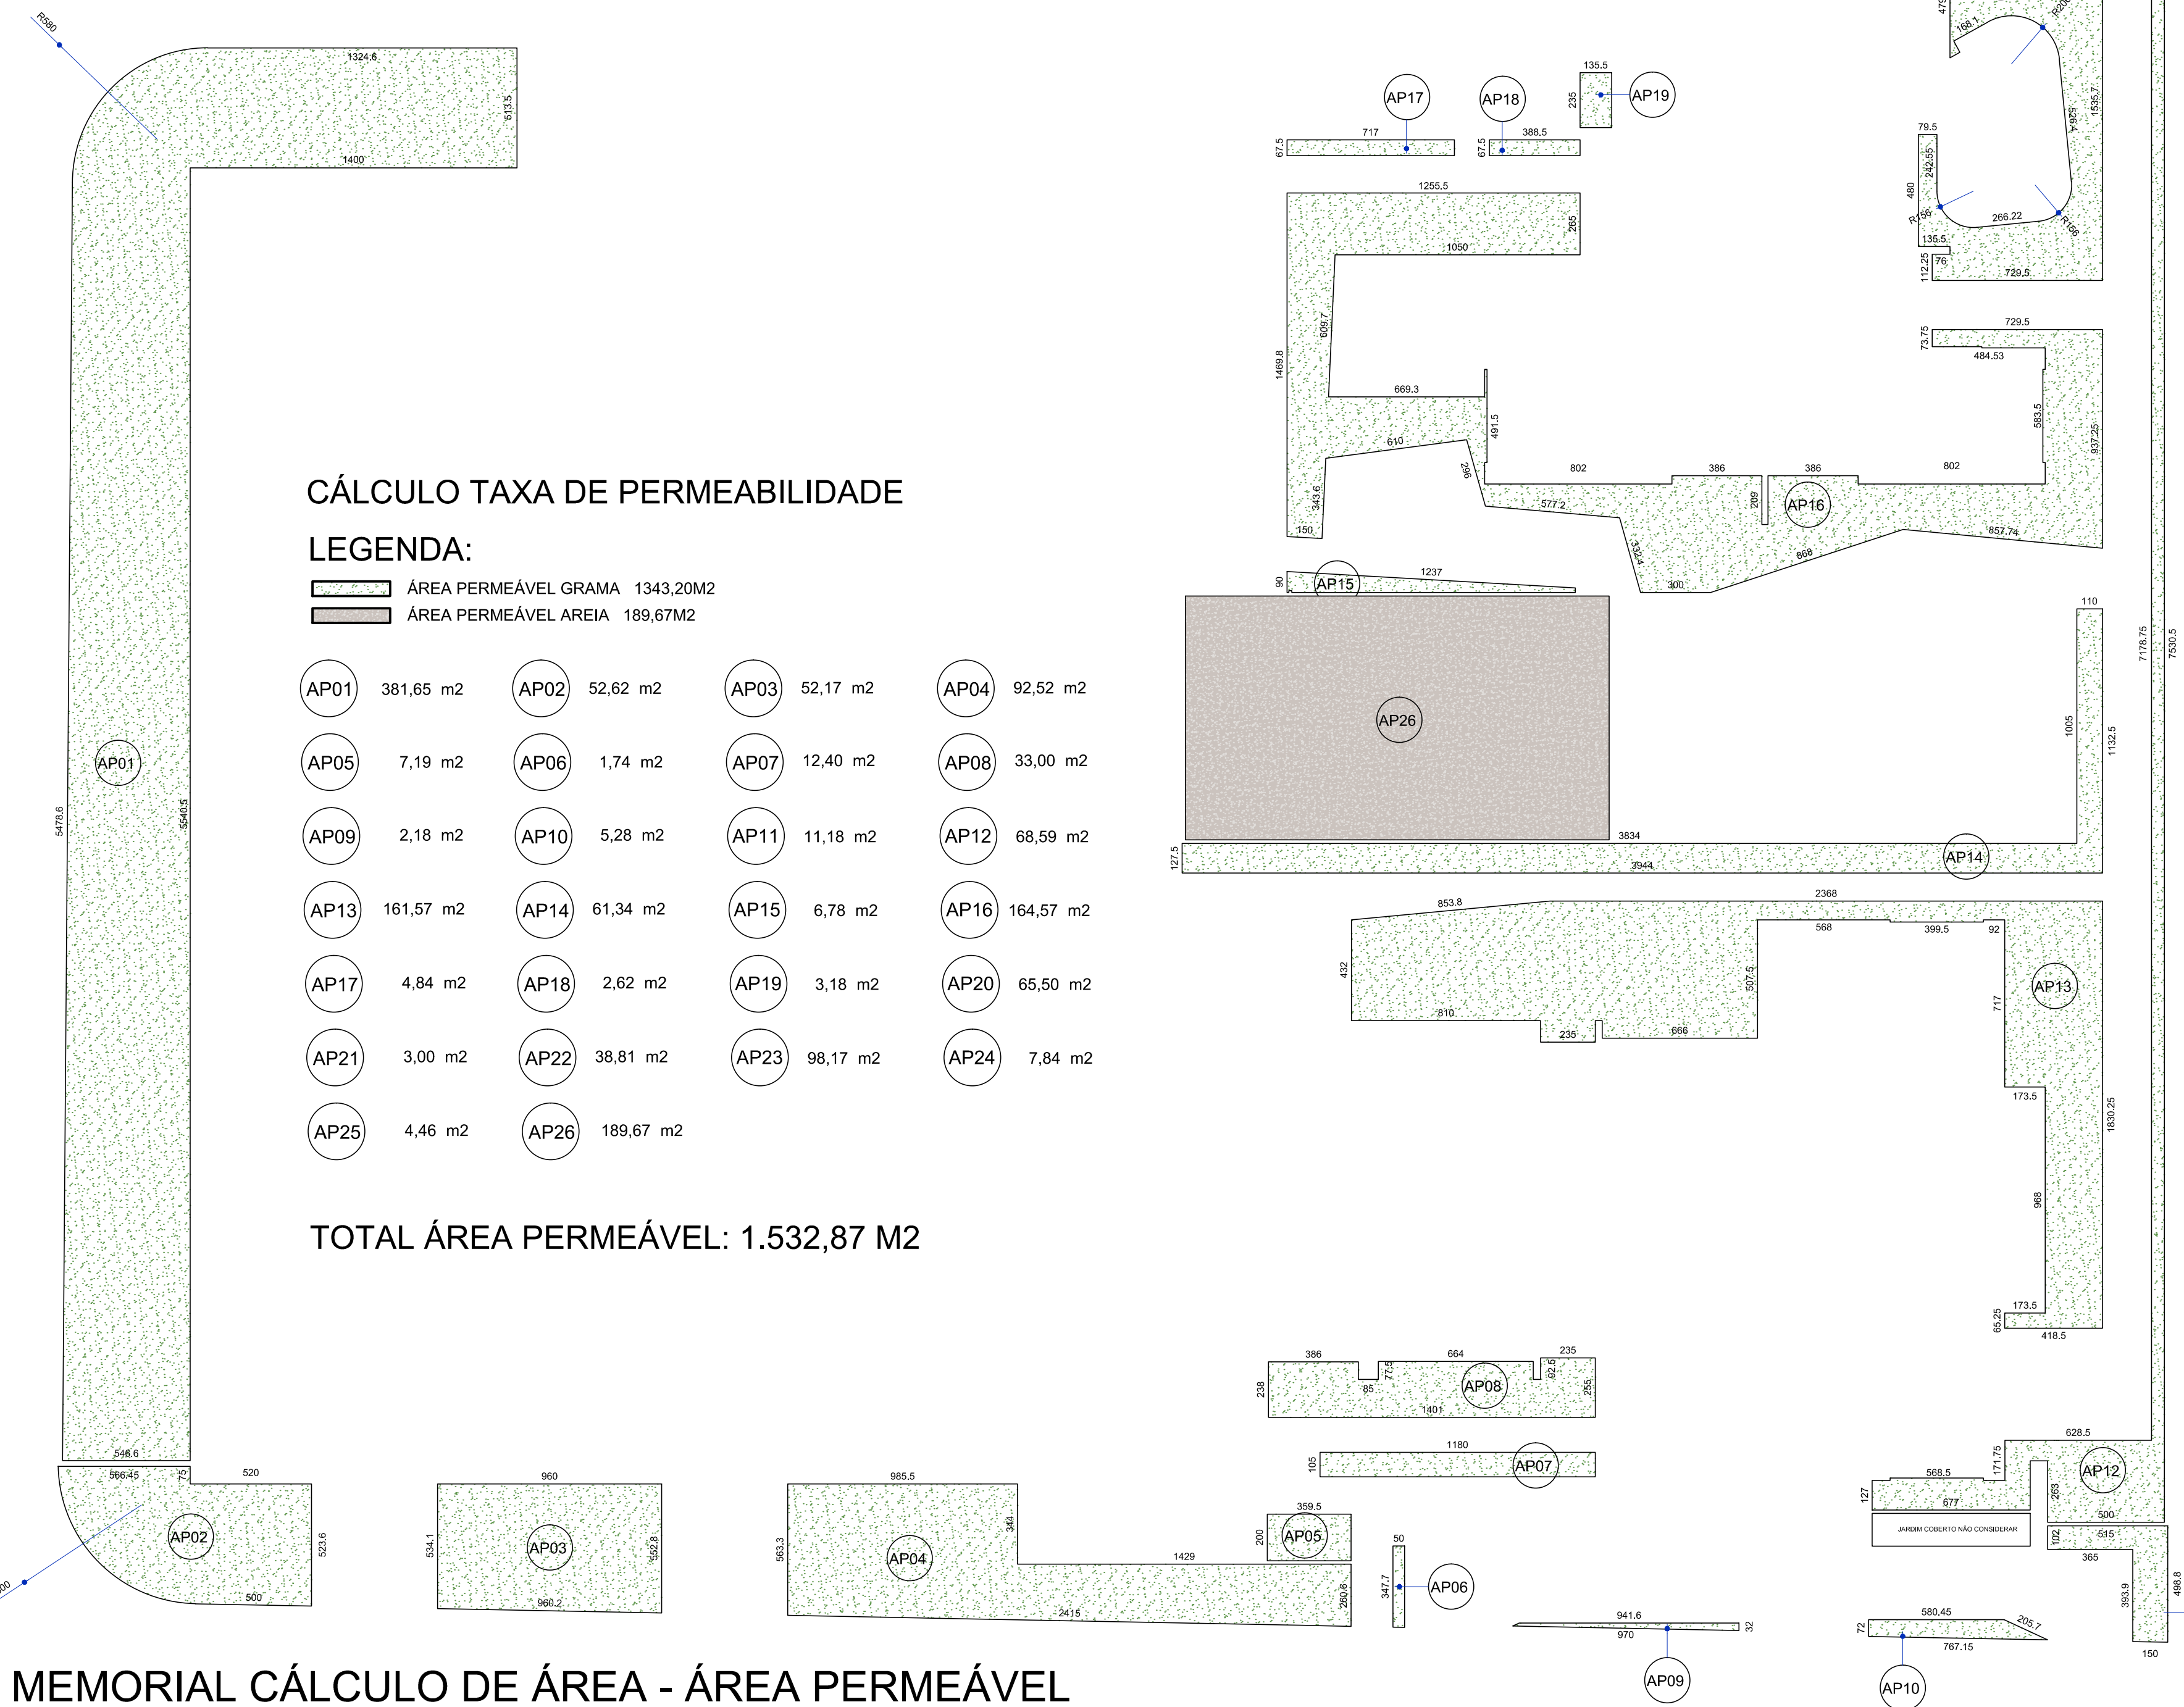

NOTA

O DEP. DE LIXO, DEP. GAS E PORTARIA 02 SÃO A TÍTULO PRECÁRIO

REVISÕES

DATA	PROCEDIMENTO
24/07/2023	ENTRECALA-PROJ
24/08/2023	ENTRECALA-PROJ

MIGUEL MAIA WYTON BRUNO RENATO MATEUS	ARQUITETO E LARABETRA - CAUI 03012-1 ARQUITETO E LARABETRA - CAUI 03012-1 ARQUITETO E LARABETRA - CAUI 03012-1
---	--

rua joão wyll 111 sf 107 - 89050-450 palhano - londrina-pr | 4330328-3991 - contato@vianarquitectura.com.br - www.vianarquitectura.com.br

YTON CONSTRUÇÃO E INCORPORAÇÃO LTDA - CÁLCULO ÁREAS DESCOBERTAS LAZER PERMEÁVELS-PREF-REB-2024

TÍTULO DA PRONCHIA	PRONCHIA	ESCALA
PROJETO ARQUITETÔNICO MEMORIAL DE CÁLCULO DE ÁREAS PERMEÁVEIS, LAZER E ÁREAS COBERTAS E DESCOBERTAS	PL06	/12

USO DA EDIFICAÇÃO	ZONEAMENTO	COEF. DE APROVEITAMENTO
CONSTRUÇÃO DE: EDIFICAÇÃO RESIDENCIAL MULTIFAMILIAR VERTICAL [RMV]	ZR7	2,91 (MÁX.3,50)

LOCAL DA OBRA	DATA DO PROJETO	TAXA DE OCUPAÇÃO
LOTE 101/A, DA SUBDIVISÃO DO LOTE 101 REMANESCENTE, SITUADO NO RIBEIRÃO DA ESPERANÇA, FAZENDA PALHANO, LONDINA-PR	24/07/2023	61,77% (MÁX. 80%)

PROPRIETÁRIO	CNPJ	INSCRIÇÃO IMOBILIÁRIA
YTON CONSTRUÇÃO E INCORPORAÇÃO LTDA	10.910.748/0001-85	06020259103960001

YTON CONSTRUÇÃO E INCORPORAÇÃO LTDA

SITUAÇÃO SEM ESCALA	BRUNO RAFAEL CATTARINO 04244617 906
---------------------	-------------------------------------

PROPRIETÁRIO: YTON CONSTRUÇÃO E INCORPORAÇÃO LTDA. CNPJ 10.910.748/0001-85

RENATO MATEUS GORNE VIANI:02635778990

RENATO MATEUS GORNE VIANI ARQUITETO E LARABETRA - CAUI 03012-1

IVANI GONCALVES DA SILVA MARIANO:6736955 3949

RESPONSÁVEL TÉCNICO PELA EXECUÇÃO DA OBRA: IVANI GONCALVES DA SILVA MARIANO. ENGENHEIRA CIVIL - OCREA PR/271110

ESPAÇO RESERVADO PARA APROVAÇÃO (Observações):

Assinatura CNP/030

DIRETORIA APROVAÇÃO DE PROJETOS Londrina, 22 de setembro de 2023. Processo Apreciação nº 18.021.328/70203-06 Nº de ORDEM: 2457/2023 Nº de ALVARÁ: 2457/2023

MARCELO PAGOTTO CARNEIRO Matrícula nº 13577-1

MARCELO PAGOTTO CARNEIRO:0 9979 16434399979

Assinado de forma digital por MARCELO PAGOTTO CARNEIRO:0 9979 16434399979