



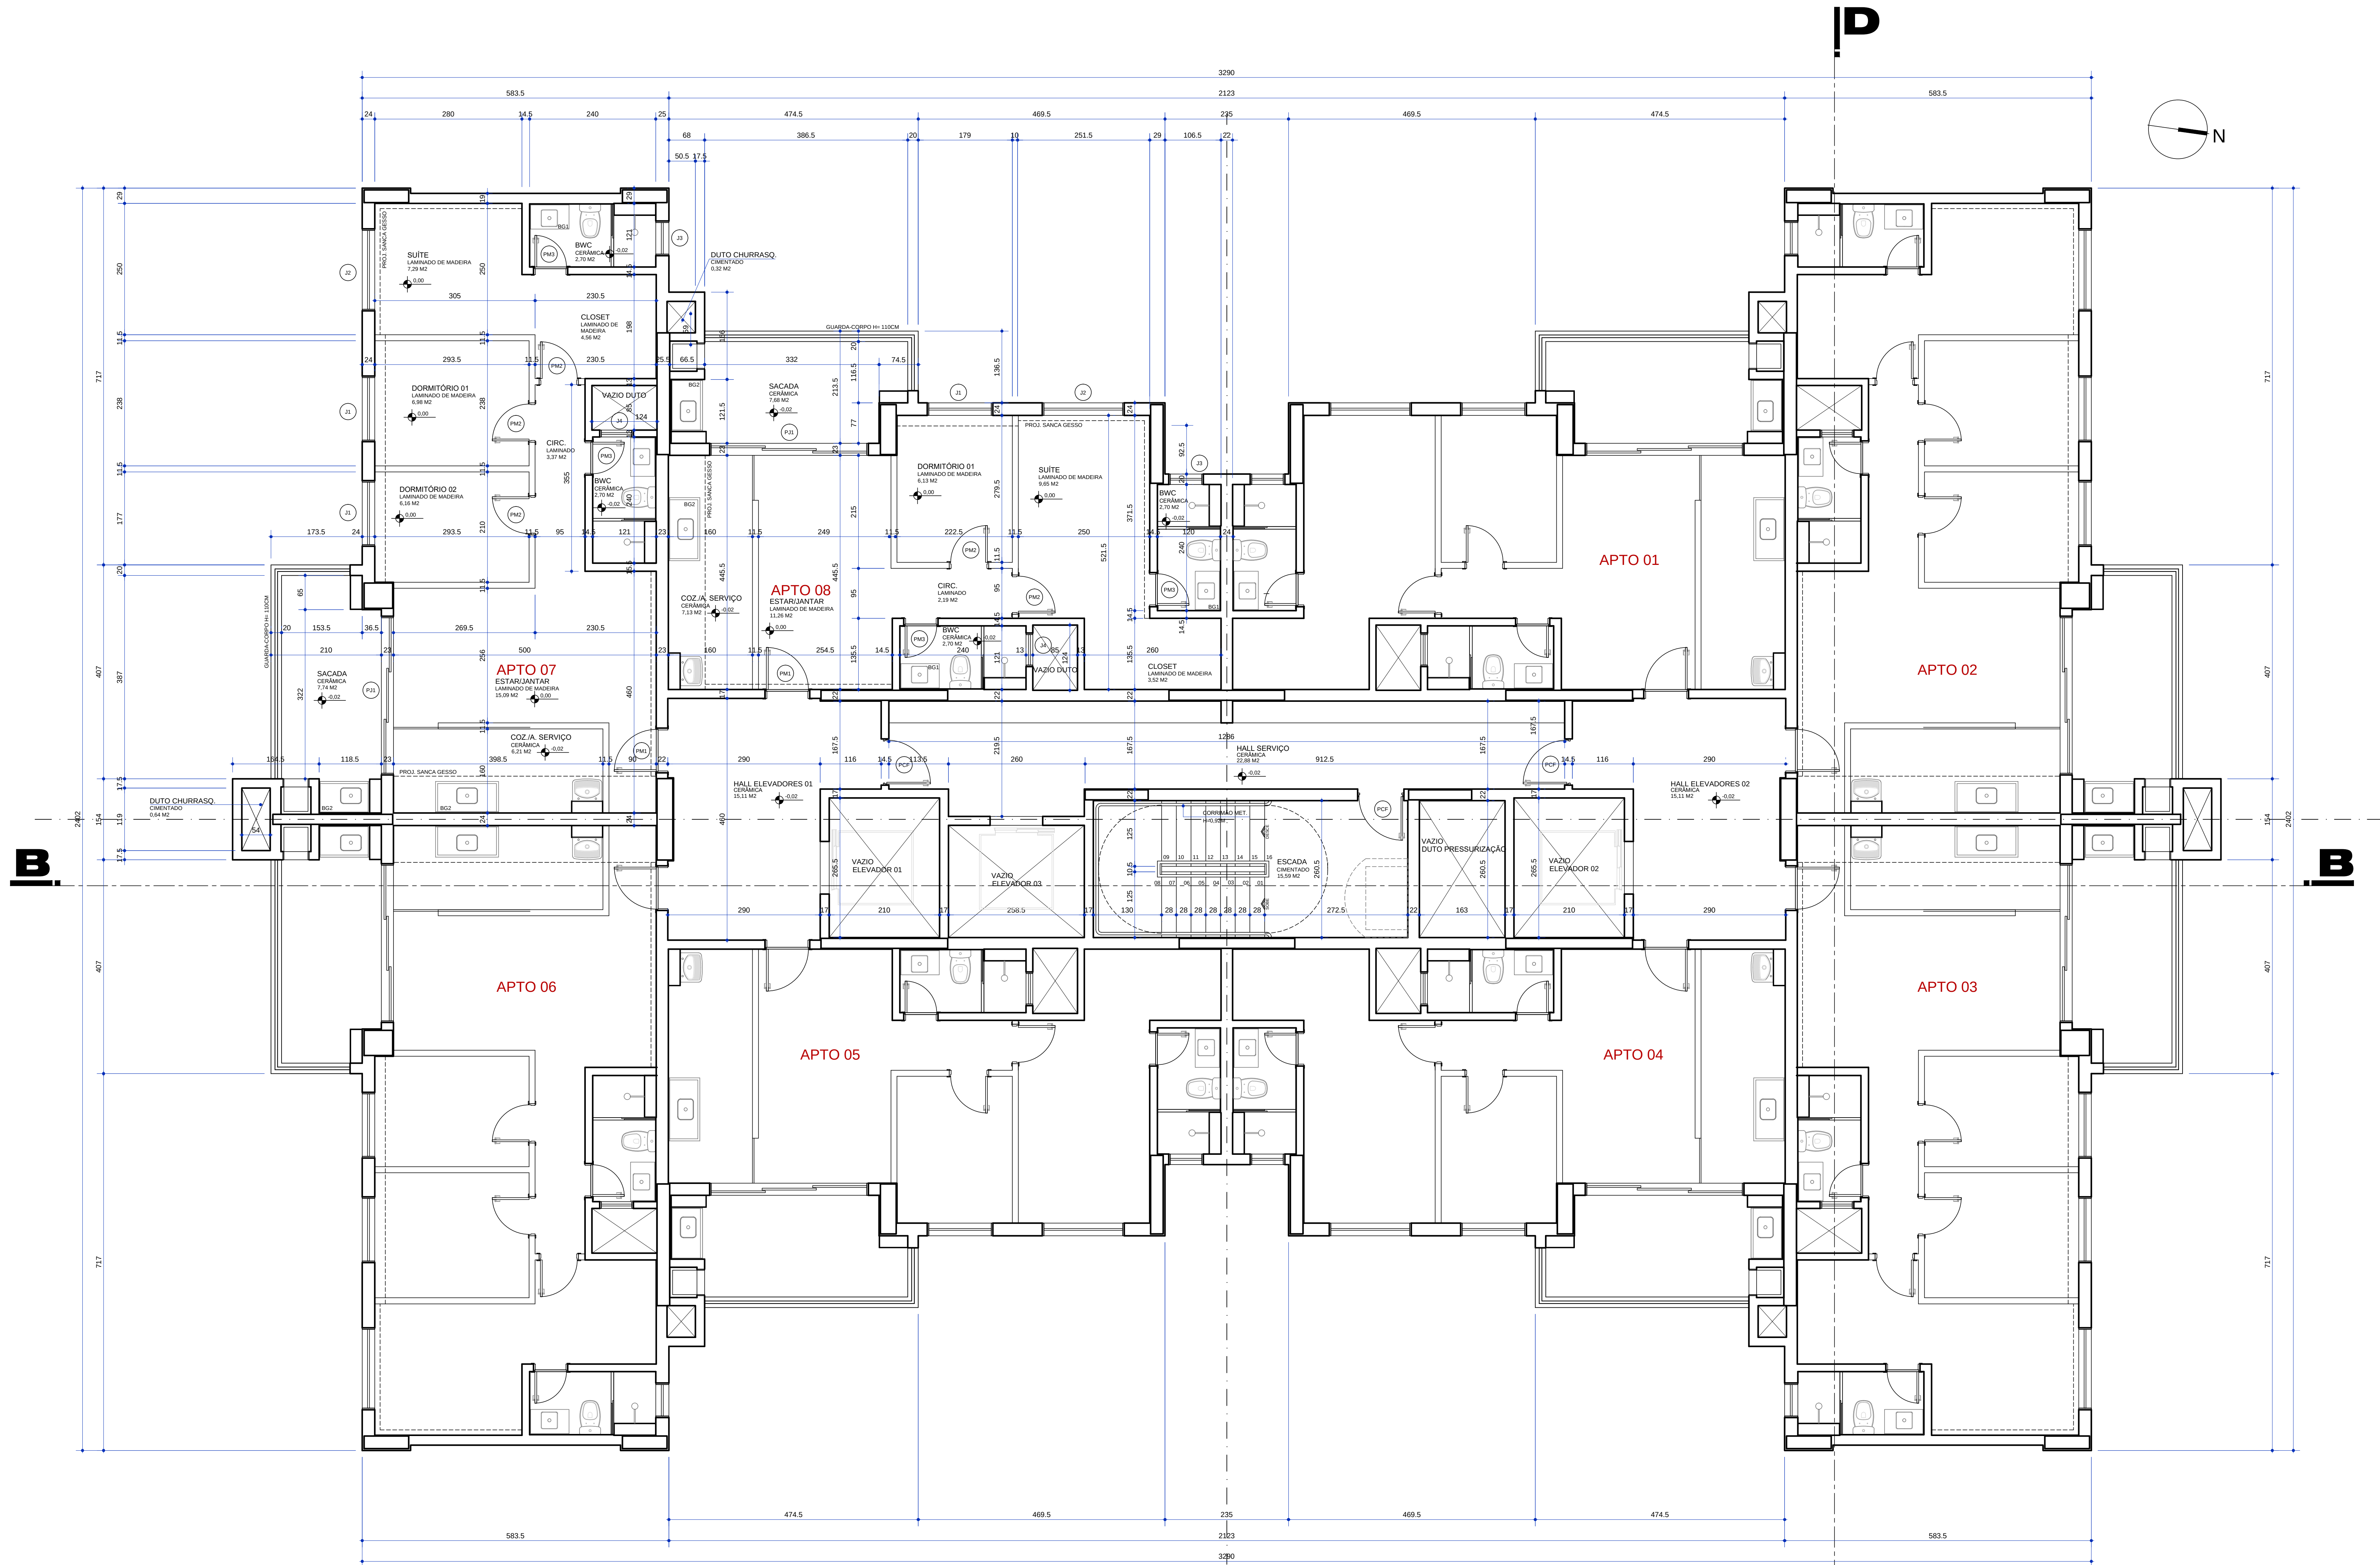

PLANTA 01° AO 20° PAVIMENTO TIPO [TORRE 02]
FIC 100
ÁREA= 694,11 m²

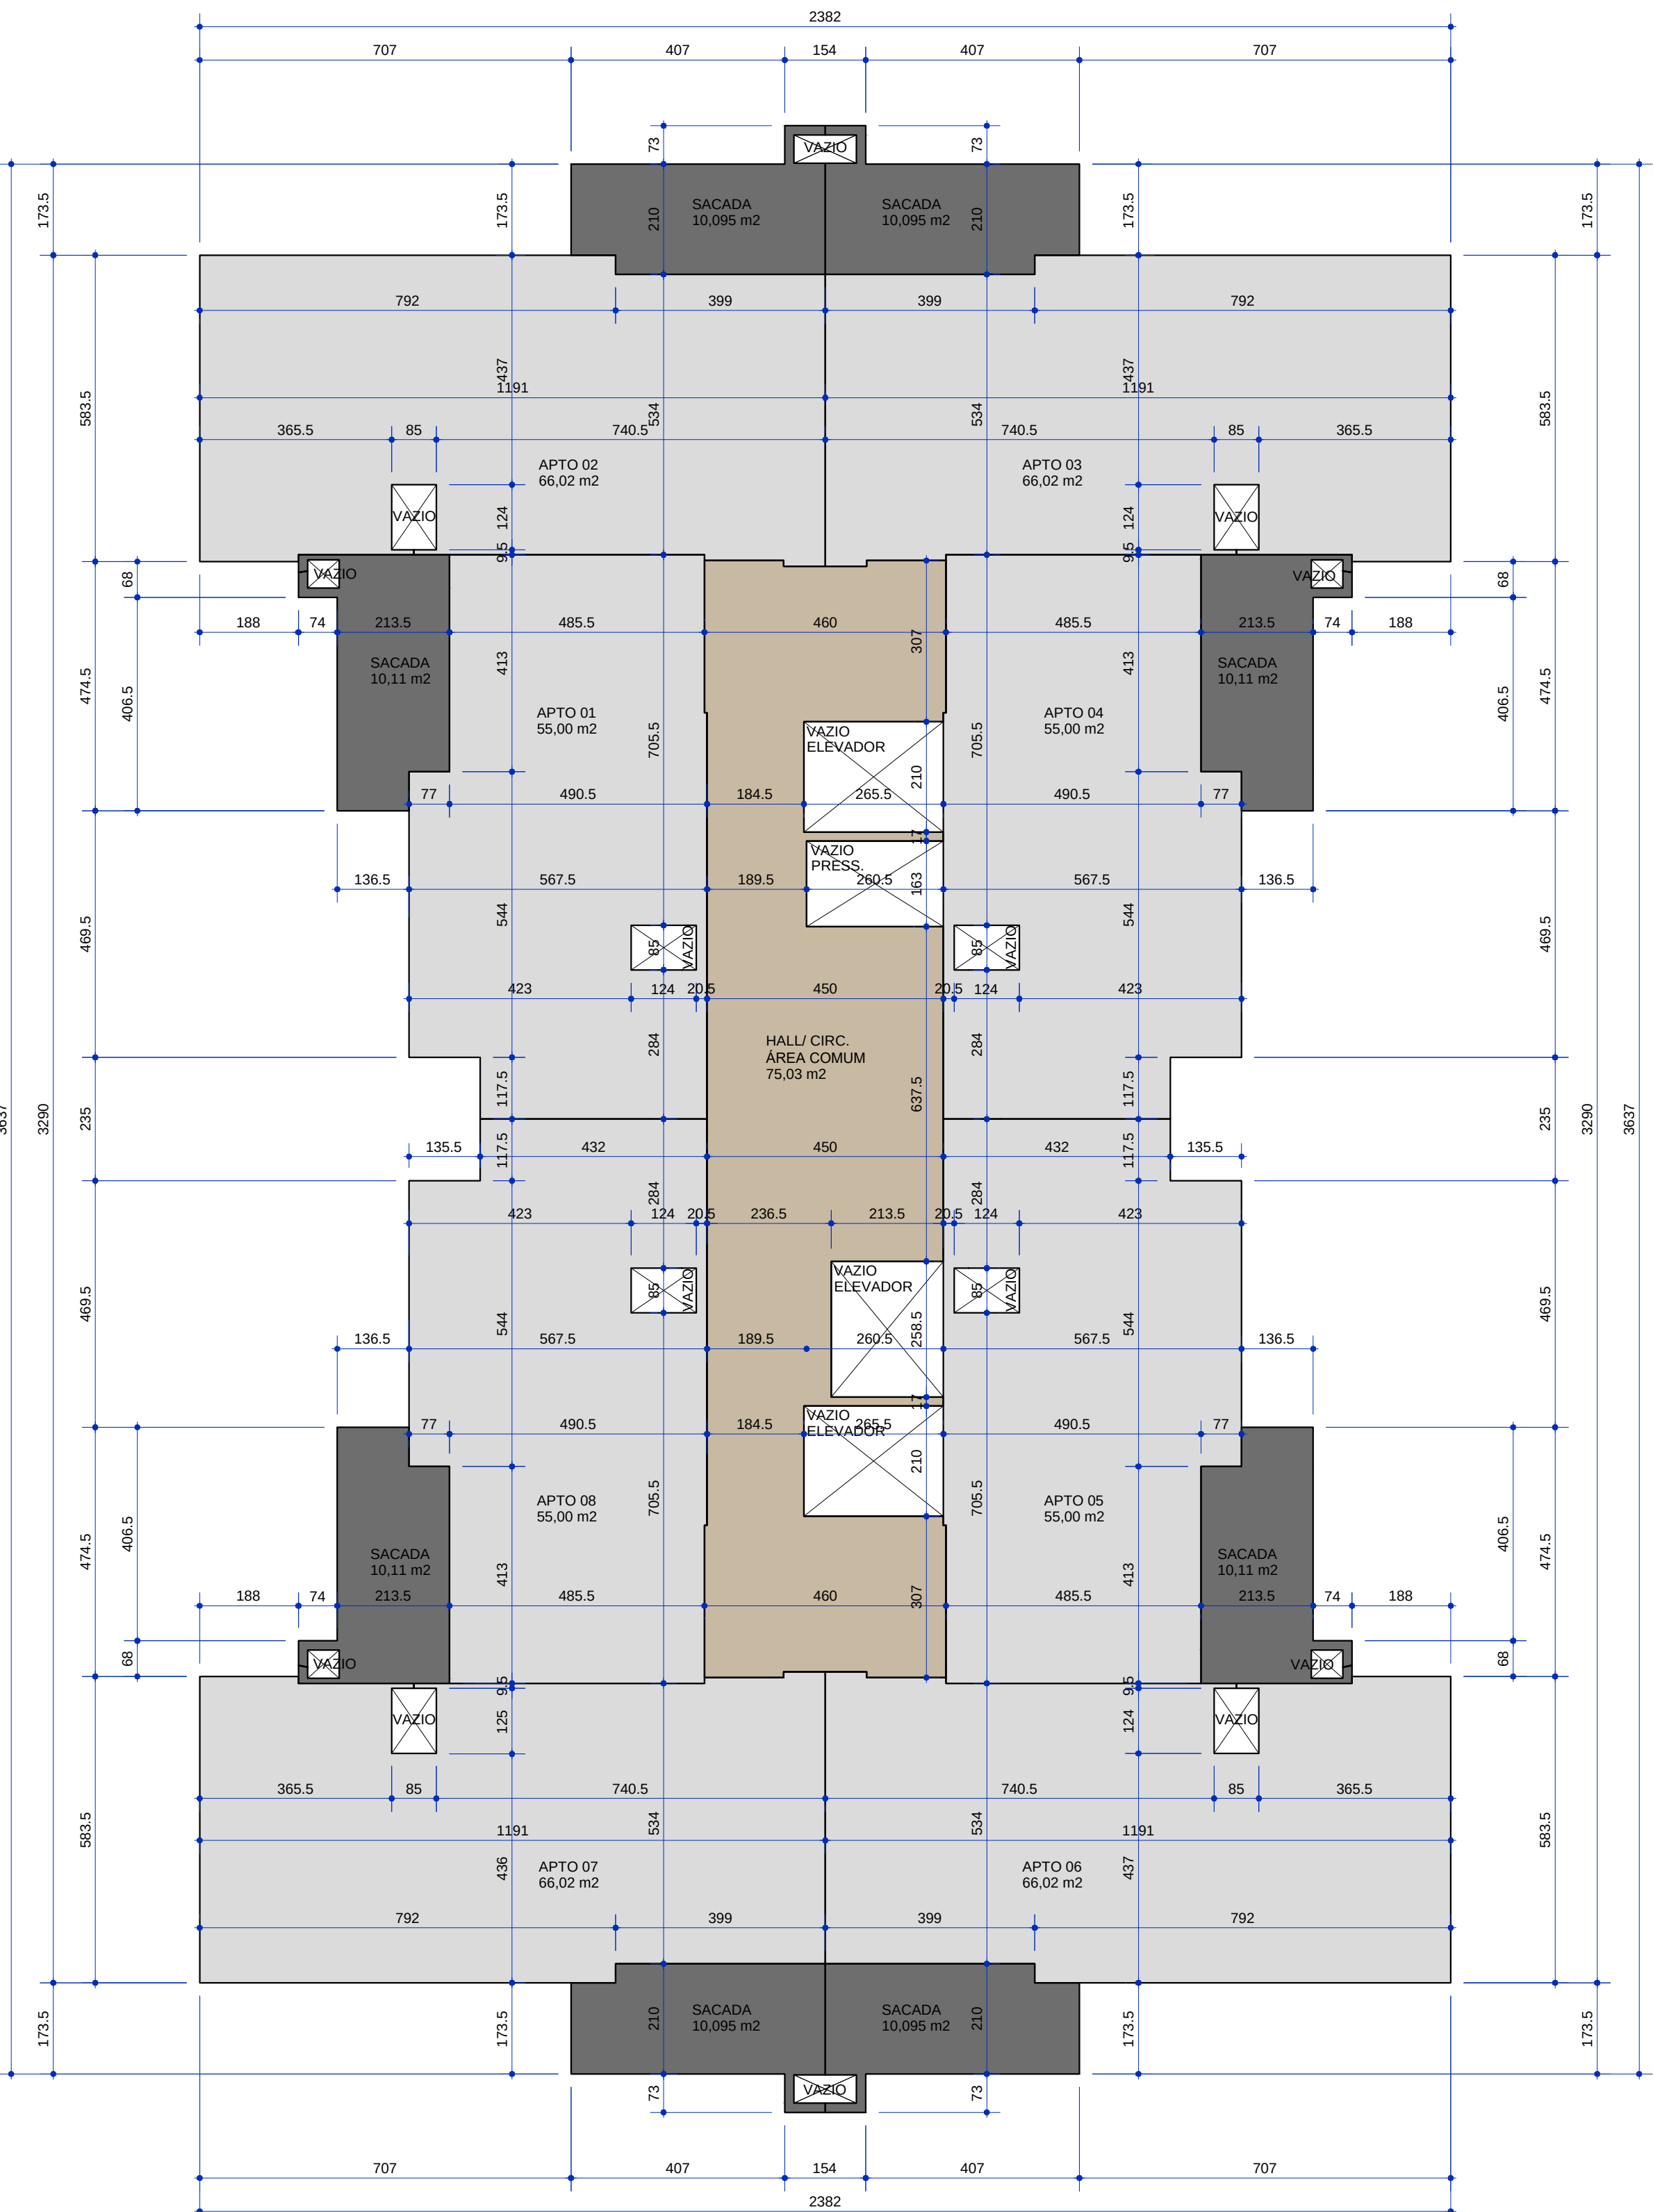

MEMORIAL CÁLCULO DE ÁREA PAV. TIPO [TORRE 02]

ÁREA = 694,11 m²

LEGENDA:

ÁREA PARA FINS DE COEFICIENTE (0,000M2 X 4) + (95,00M2 X 4) =	484,08M2
ÁREA SACADA (10,00M2 X 4) + (10,09M2 X 4) =	80,82M2
ÁREA COMUM =	75,03M2
ÁREA TOTAL PRIVATIVA =	564,90M2
TOTAL =	639,93M2

QUADRO DE ESQUADRIAS TORRE RESIDENCIAL									
COD.	NOMINAL	LARGURA	ALTURA	PERÍMETRO	ABERTURA	VÍDEO	OBSERVAÇÕES		
J1	JANELA ALUMINIO	110	135	130	CORRENVENZ	INCOLOM	ACABAMENTO ALUMINIO ARARANHA-CEU E790		
J2	JANELA ALUMINIO	150	135	130	CORRENVENZ	INCOLOM	ACABAMENTO ALUMINIO ARARANHA-CEU E790		
J3	JANELA ALUMINIO	090	065	100	BASULANTE	VÍD FANTASIA	ACABAMENTO ALUMINIO ARARANHA-CEU E790		
J4	JANELA ALUMINIO	090	065	100	BASULANTE	VÍD FANTASIA	ACABAMENTO ALUMINIO ARARANHA-CEU E790		
J5	JANELA ALUMINIO	225	065				TELA ARANHA 3MM EM MALHA 2,5X2,5CM		
J6	JANELA ALUMINIO	120	040	4180	FIXO		VENEZIANA ALUMINIO ARARANHA-CEU E790		
P01	PORTA MADEIRA	090	235	-	ABRIR	-	PINTURA COF BRANCO		
P02	PORTA MADEIRA	070	235	-	ABRIR	-	PINTURA COF BRANCO		
P03	PORTA MADEIRA	090	235	-	ABRIR	-	PINTURA COF BRANCO		
P04	PORTA ALUMINIO	296	235	-	CORRER	INCOLOM	ACABAMENTO ALUMINIO ARARANHA-CEU E790		
P05	PORTA ALUMINIO	090	235	-	ABRIR	-	ACABAMENTO ALUMINIO ARARANHA-CEU E790		
P06	PORTA ALUMINIO	070	145	-	ABRIR	-	ACABAMENTO ALUMINIO ARARANHA-CEU E790		
P07	PORTA ALUMINIO	090	235	-	ABRIR	-	ACABAMENTO ALUMINIO ARARANHA-CEU E790		
P08	PORTA COFCA FOSCO	090	235	-	ABRIR	-	BOLAS DE VÁCUO		

CONVENÇÕES

- B01 BANCADA GRANITO-H=85 CM
VER DETALHAMENTO
B02 BANCADA GRANITO-H=80 CM
VER DETALHAMENTO
B03 BANCADA GRANITO-H=105 CM
VER DETALHAMENTO

REVISÕES

DATA	PROCEDIMENTO
24/07/2023	ENTREGA PROJ

PROJETO: TORRE 02
PROJETO: TORRE 02
TÍTULO DA PRONAMIA
PROJETO ARQUITETÔNICO
PLANTA PAV. TIPO TORRE 02
USO DA EDIFICAÇÃO
CONSTRUÇÃO DE
EDIFICAÇÃO RESIDENCIAL MULTIFAMILIAR VERTICAL (RMV)
LOCAL DA OBRA
LOTE 101/A, DA SUBDIVISÃO DO LOTE 101 REMANESCENTE,
SITUADO NO RIBEIRÃO DA ESPERANÇA, FAZENDA PALHANO,
LONDREIRA-PR
PROPRIETÁRIO
YTICON CONSTRUÇÃO E INCORPORAÇÃO LTDA
SITUAÇÃO: SEM ESCALA - VER PRONAMIA PLT

PRONAMIA
PL09
/12
INDICADAS
COEF. DE APROVEITAMENTO
2,91
(MÁX: 3,50)
DATA DO PROJETO
24/07/2023
TAXA DE OCUPAÇÃO
61,77%
(MÁX: 80%)
CNPJ
10.910.748/0001-85
INSCRIÇÃO ESTADUAL
06020259103960001
DECLARAÇÃO DE APROVAÇÃO DO PROJETO NÃO NULIFICA
O RECONHECIMENTO POR PARTE DA PREFEITURA DO DIREITO DE
PROPRIEDADE DO TERRENO

BRUNO
RAFAEL
CATARINO
4244617906
14/08/10-03/07
Assinado de forma
digital por BRUNO
RAFAEL
CATARINO
4244617906
14/08/10-03/07
PROPRIETÁRIO
YTICON CONSTRUÇÃO E INCORPORAÇÃO LTDA
CNPJ 10.910.748/0001-85
RENATO
MATEUS GORNE
VIANI:02635778
990
Assinado de forma
digital por RENATO
MATEUS GORNE
VIANI:02635778
990
11/02/25-03/07
AUTOR DO PROJETO
RENATO MATEUS GORNE VIANI
ARQUITETO E URBANISTA - CRI 408693
IVANI GONCALVES
DA SILVA
MARIANO:6736955
3949
Assinado de forma
digital por IVANI
GONCALVES DA SILVA
MARIANO:6736955
3949
14/04/15-03/07
RESPONSÁVEL TÉCNICO PELA EXECUÇÃO DA OBRA
DIRCEU MARIA DA SILVA
ENGENHEIRA CIVIL - CREA PR 6412320
ESPACIO RESERVADO PARA APROVAÇÃO (Observações)

DIRETORIA APROVAÇÃO DE PROJETOS
Londrina, 22 de setembro de 2022.
Processo Aproveitamento nº 18.021.1287/2022-06
Nº de ORDEM: 2457/2023
Nº de ALVARÁ: 2457/2023
MARCELO PAGOTTO CARNEIRO
Matrícula nº 13917-1
Assinado de forma
digital por
MARCELO PAGOTTO
CARNEIRO:01643439
979
Dado: 2023.09.27
13:15:47 -03'00'