




CÁLCULO ÁREA DE LAZER MÍNIMA	
(1º AO 20º) PAV. TIPO - 66,02 X 160 APTOS	10.563,20
(1º AO 20º) PAV. TIPO - 65,985 X 80 APTOS	5.278,80
(1º AO 20º) PAV. TIPO - 55,00 X 80 APTOS	4.400,00
ÁREA PRIVATIVA COMPUTÁVEL TOTAL	20.242,00
Am = ÁREA MÍNIMA = 10% DA ÁREA COMPUTÁVEL	2.024,20
ÁREA DE LAZER COBERTA DO PROJETO	1.275,94
ÁREA DE LAZER DESCOBERTA DO PROJETO	1.989,19
ÁREA DE LAZER TOTAL	3.265,13

LEGENDA:

- ÁREA DE LAZER COBERTA PAV. TÉRREO = 1.275,94m2
- ÁREA DE LAZER DESCOBERTA PAV. TÉRREO = 1.989,19m2

PAV. NÍVEL 579,25 [TÉRREO]

TOTAL TÉRREO COBERTO: (ÁREA PARA CÁLCULO DE TAXA DE OCUPAÇÃO)	
TOTAL	4.211,29 m2
DESCOBERTAS:	
CIRCULAÇÃO GARAGEM	58,69 m2
CIRCULAÇÃO PEDESTRES	933,60 m2
QUADRAS	347,95 m2
PISCINAS	87,70 m2
TOTAL	1.427,94 m2
TOTAL PAV. NÍVEL 579,25 [TÉRREO] (COBERTO+DESCOBERTO)	5.639,23 m2

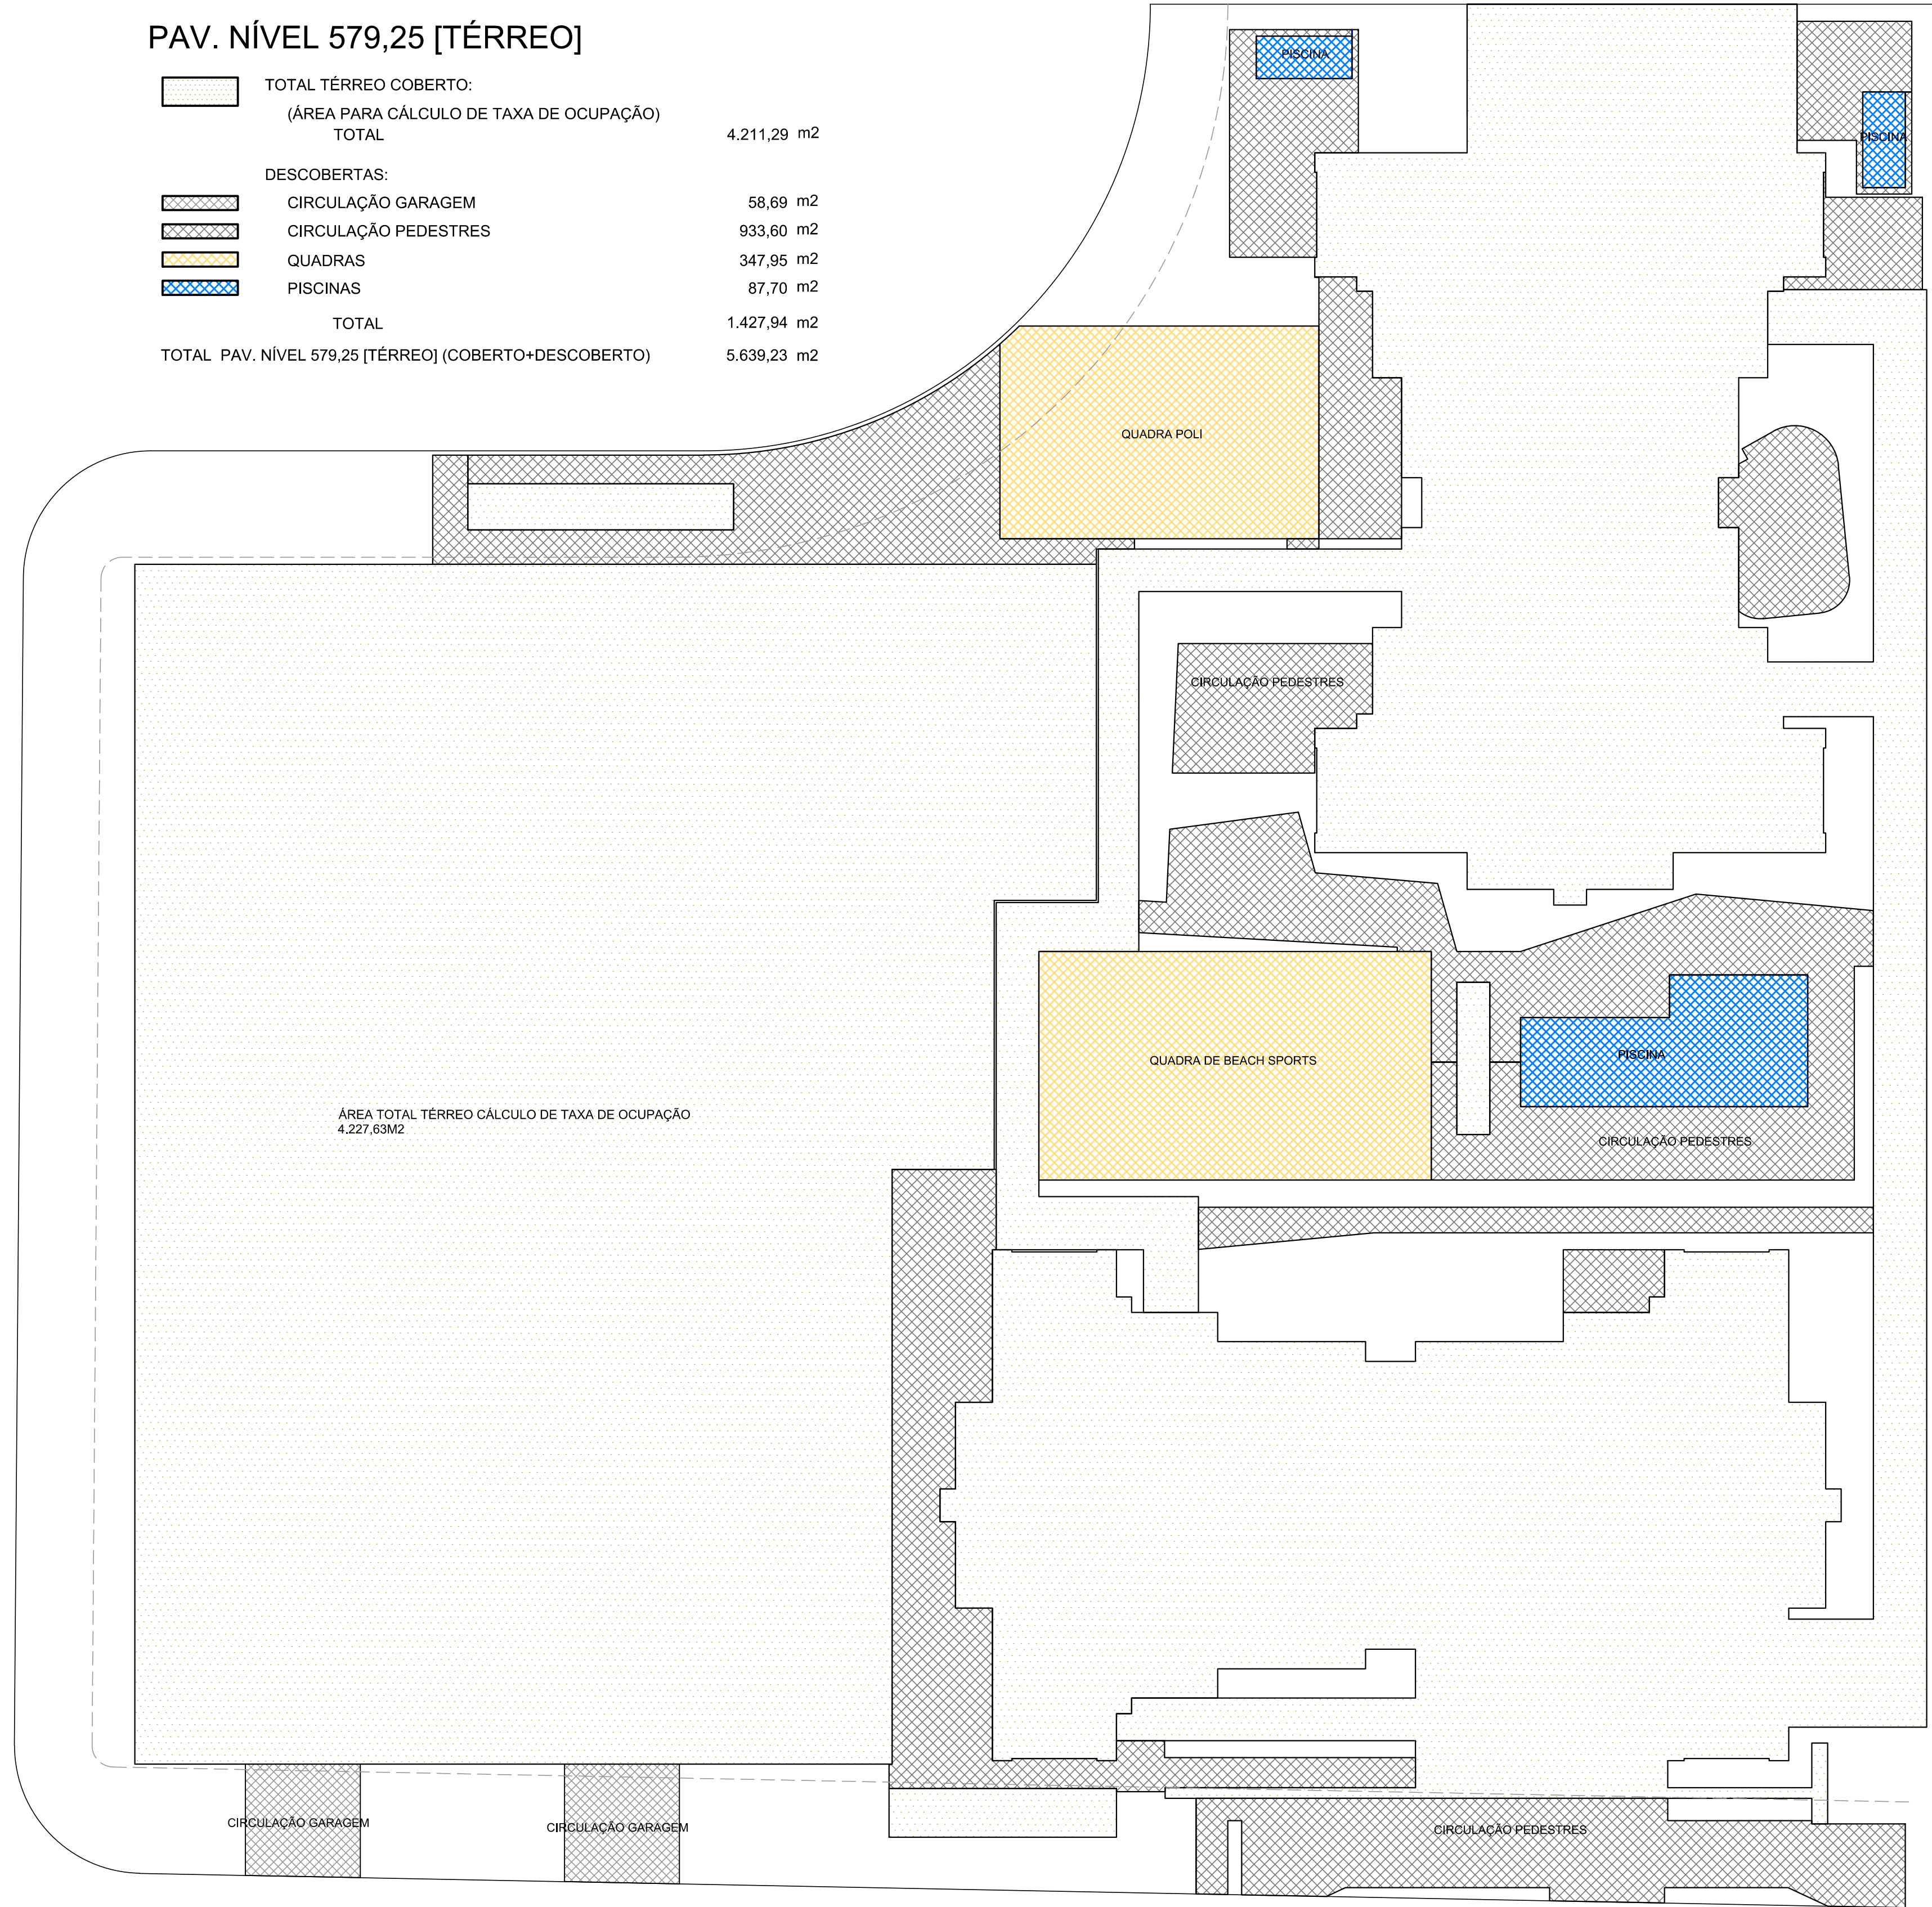

MEMORIAL CÁLCULO DE ÁREA - ÁREAS COBERTAS E DESCOBERTAS TÉRREO (NÍVEL 579,25)

ESC. 1:200


CÁLCULO TAXA DE PERMEABILIDADE

LEGENDA:

- ÁREA PERMEÁVEL GRAMA 1343,20M2
- ÁREA PERMEÁVEL AREIA 189,67M2

AP01 381,65 m2	AP02 52,62 m2	AP03 52,17 m2	AP04 92,52 m2
AP05 7,19 m2	AP06 1,74 m2	AP07 12,40 m2	AP08 33,00 m2
AP09 2,18 m2	AP10 5,28 m2	AP11 11,18 m2	AP12 68,59 m2
AP13 161,57 m2	AP14 61,34 m2	AP15 6,78 m2	AP16 164,57 m2
AP17 4,84 m2	AP18 2,62 m2	AP19 3,18 m2	AP20 65,50 m2
AP21 3,00 m2	AP22 38,81 m2	AP23 98,17 m2	AP24 7,84 m2
AP25 4,46 m2	AP26 189,67 m2		

TOTAL ÁREA PERMEÁVEL: 1.532,87 M2

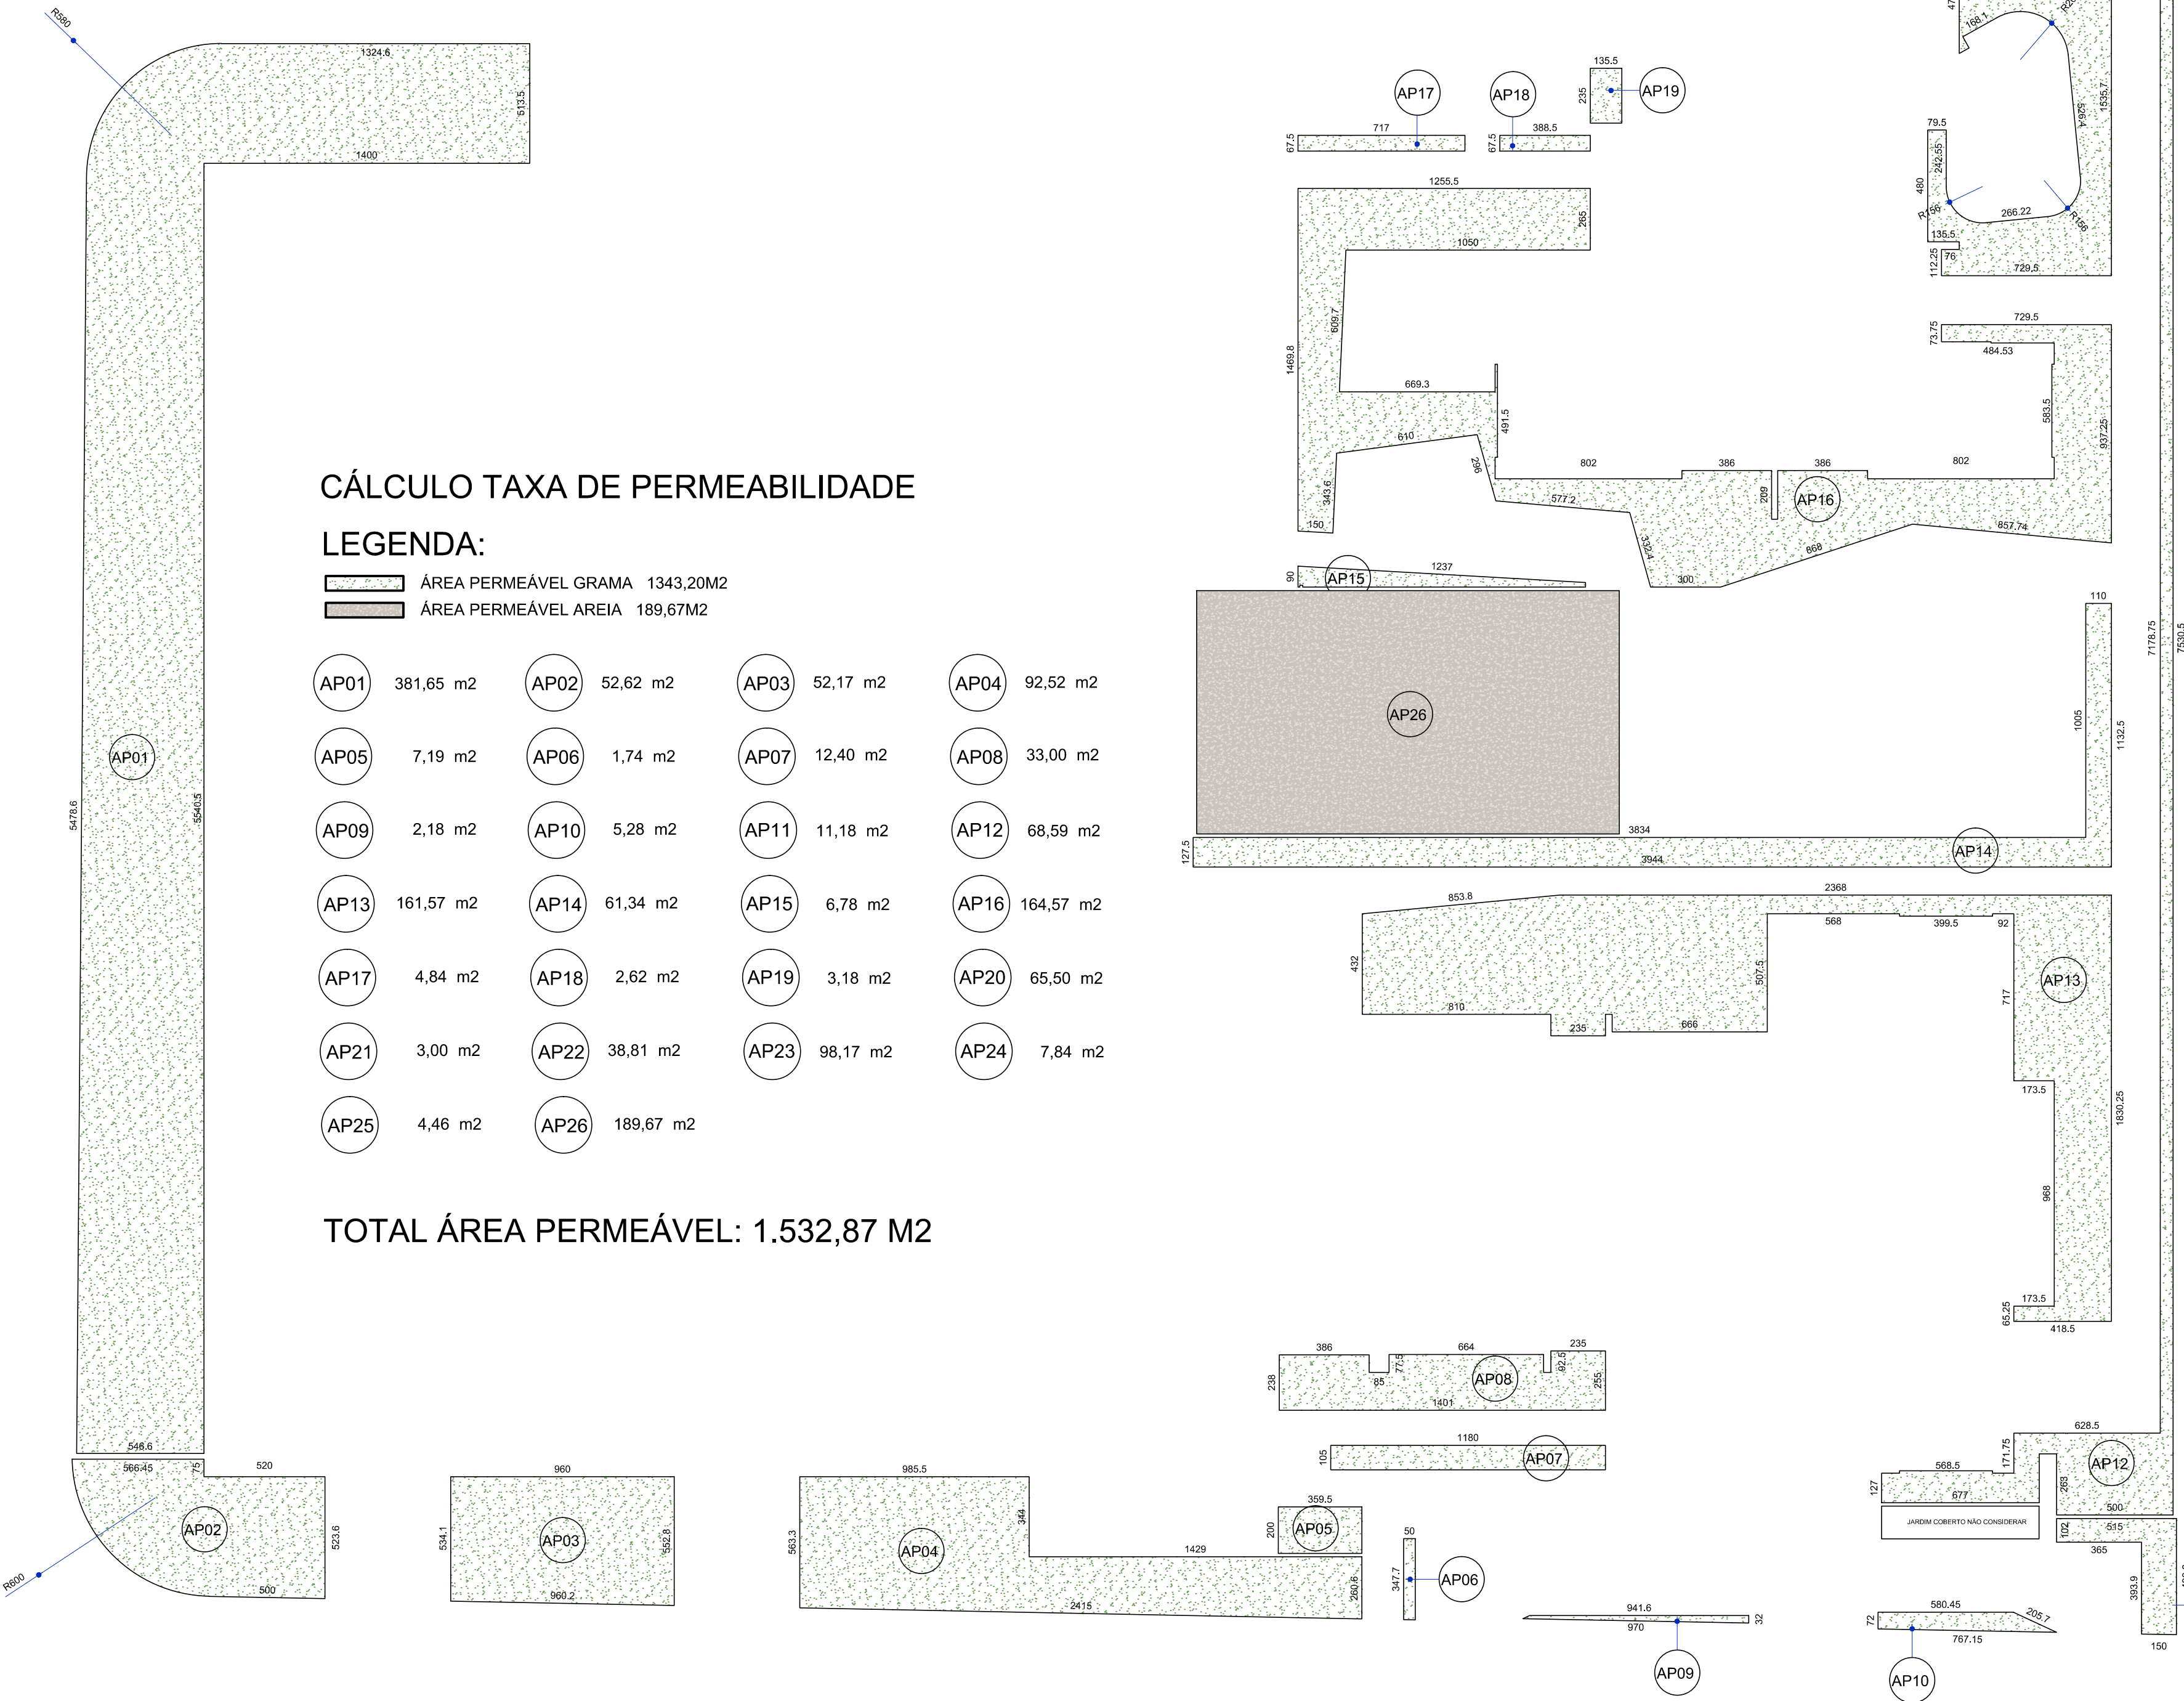

MEMORIAL CÁLCULO DE ÁREA - ÁREA PERMEÁVEL

ESC. 1:200

NOTA

O DEP. DE LÍQU. DEP. GÁS E PORTARIA 02 SÃO A TÍTULO PRECÁRIO

REVISÕES

DATA	PROCEDIMENTO
24/07/2023	ENTREGA-R00
24/08/2023	ENTREGA-R01

MEUCL VIANI
VITOR ORIOLO
RÉNATO VIANI

ARQUITETO E URBANISTA - CAAU 430278
ARQUITETO E URBANISTA - CAAU 430278
ARQUITETO E URBANISTA - CAAU 430278

viani

nua joão wyelf 111 al 107 - 86059-450 palhano - londrina-pr | contato@vianiarquitetura.com.br | www.vianiarquitetura.com.br

YITICON CONSTRUÇÃO E INCORPORAÇÃO LTDA. CÁLCULO ÁREAS DESCOBERTAS LAZER PLANEJADAS (PAV. NÍVEL 579,25)

TÍTULO DA PRANCHA: PROJETO ARQUITETÔNICO MEMORIAL DE CÁLCULO DE ÁREAS PERMEÁVEIS, LAZER E ÁREAS COBERTAS E DESCOBERTAS	PRANCHA PL05 /12	ESCALA INDICADAS 2,91 (MÁX.3,50)
USO DA EDIFICAÇÃO CONSTRUÇÃO DE: EDIFICAÇÃO RESIDENCIAL MULTIFAMILIAR VERTICAL [RMV] LOTE 101A, DA SUBDIVISÃO DO LOTE 101 REMANESCENTE, SITUADO NO RIBEIRÃO DA ESPERANÇA, FAZENDA PALHANO, LONDINA-PR	ZONAMENTO ZR7	COEF. DE APROVEITAMENTO 2,91 (MÁX.3,50)
PROPRIETÁRIO YITICON CONSTRUÇÃO E INCORPORAÇÃO LTDA. CNPJ 10.910.748/0001-85	DATA DO PROJETO 24/07/2023	TAXA DE OCUPAÇÃO 61,77% (MÁX. 80%)
SITUAÇÃO SEM ESCALA	INSCRIÇÃO IMOBILIAR 06020259103960001	

DECLARO QUE A APROVAÇÃO DO PROJETO NÃO IMPLICA NO RECONHECIMENTO POR PARTE DA PREFEITURA DO DIREITO DE PROPRIEDADE DO TERRENO.	BRUNO RAFAEL CATARINO 4244617906 Data: 2023.09.25 16:24:38 -03'00'
PROPRIETÁRIO YITICON CONSTRUÇÃO E INCORPORAÇÃO LTDA. CNPJ 10.910.748/0001-85	Assinado de forma digital por BRUNO RAFAEL CATARINO 4244617906 Data: 2023.09.25 16:24:38 -03'00'
RENATO MATEUS GORNE VIANI:026357789 90	Assinado de forma digital por RENATO MATEUS GORNE VIANI:02635778990 Data: 2023.08.24 11:18:23 -03'00'
AUTOR DO PROJETO RENATO MATEUS GORNE VIANI ARQUITETO E URBANISTA - CAAU 430632-9	Assinado de forma digital por IVANI GONCALVES DA SILVA MARIANO:673695 Data: 2023.09.25 17:03:26 -03'00'

QUADRO DE ÁREAS - VER PRANCHA PLUS	IVANI GONCALVES DA SILVA MARIANO:673695 53949
RESPONSÁVEL TÉCNICO PELA EXECUÇÃO DA OBRA IVANI GONCALVES DA SILVA MARIANO ENGENHEIRA CIVIL - CREA PR-27111-0	Assinado de forma digital por IVANI GONCALVES DA SILVA MARIANO:673695 Data: 2023.09.25 17:03:26 -03'00'

DIRETORIA APROVAÇÃO DE PROJETOS Londrina, 22 de setembro de 2023. Processo Aprovação nº 19.021.12878/2023-06 Nº de ORDEM: 2457/2023 Nº de ALVARÁ: 2457/2023	Assinatura Eletrônica
MARCELO PAGOTTO CARNEIRO Matrícula nº 13577-3	