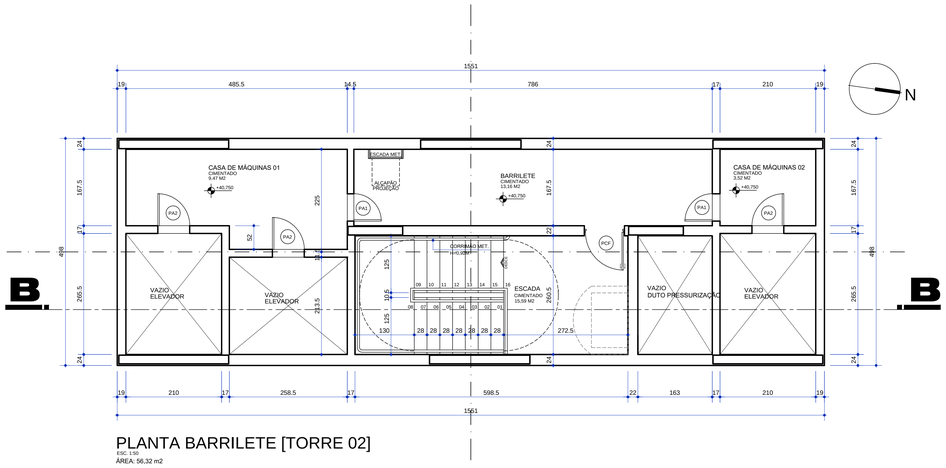

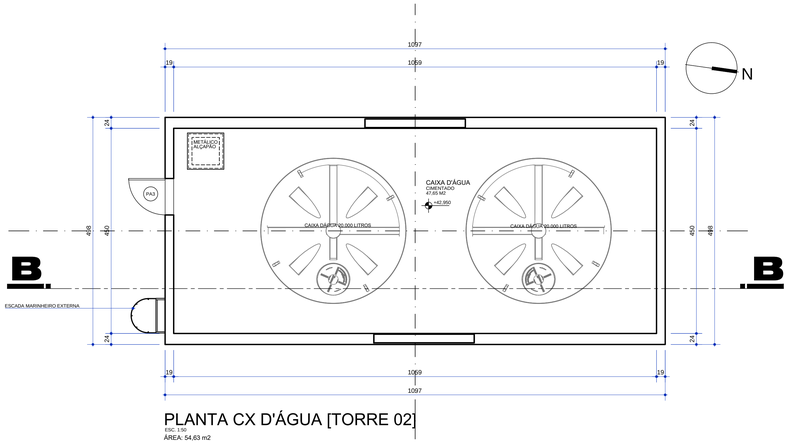

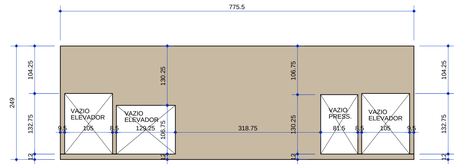

MEMORIAL CÁLCULO DE ÁREA
BARRILETE [TORRE 02]
ESC. 1:100
ÁREA = 56,32 m2

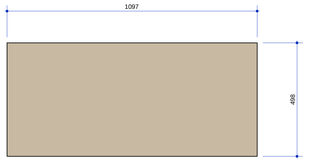

MEMORIAL CÁLCULO DE ÁREA
CAIXA D'ÁGUA [TORRE 02]
ESC. 1:100
ÁREA = 54,63 m2

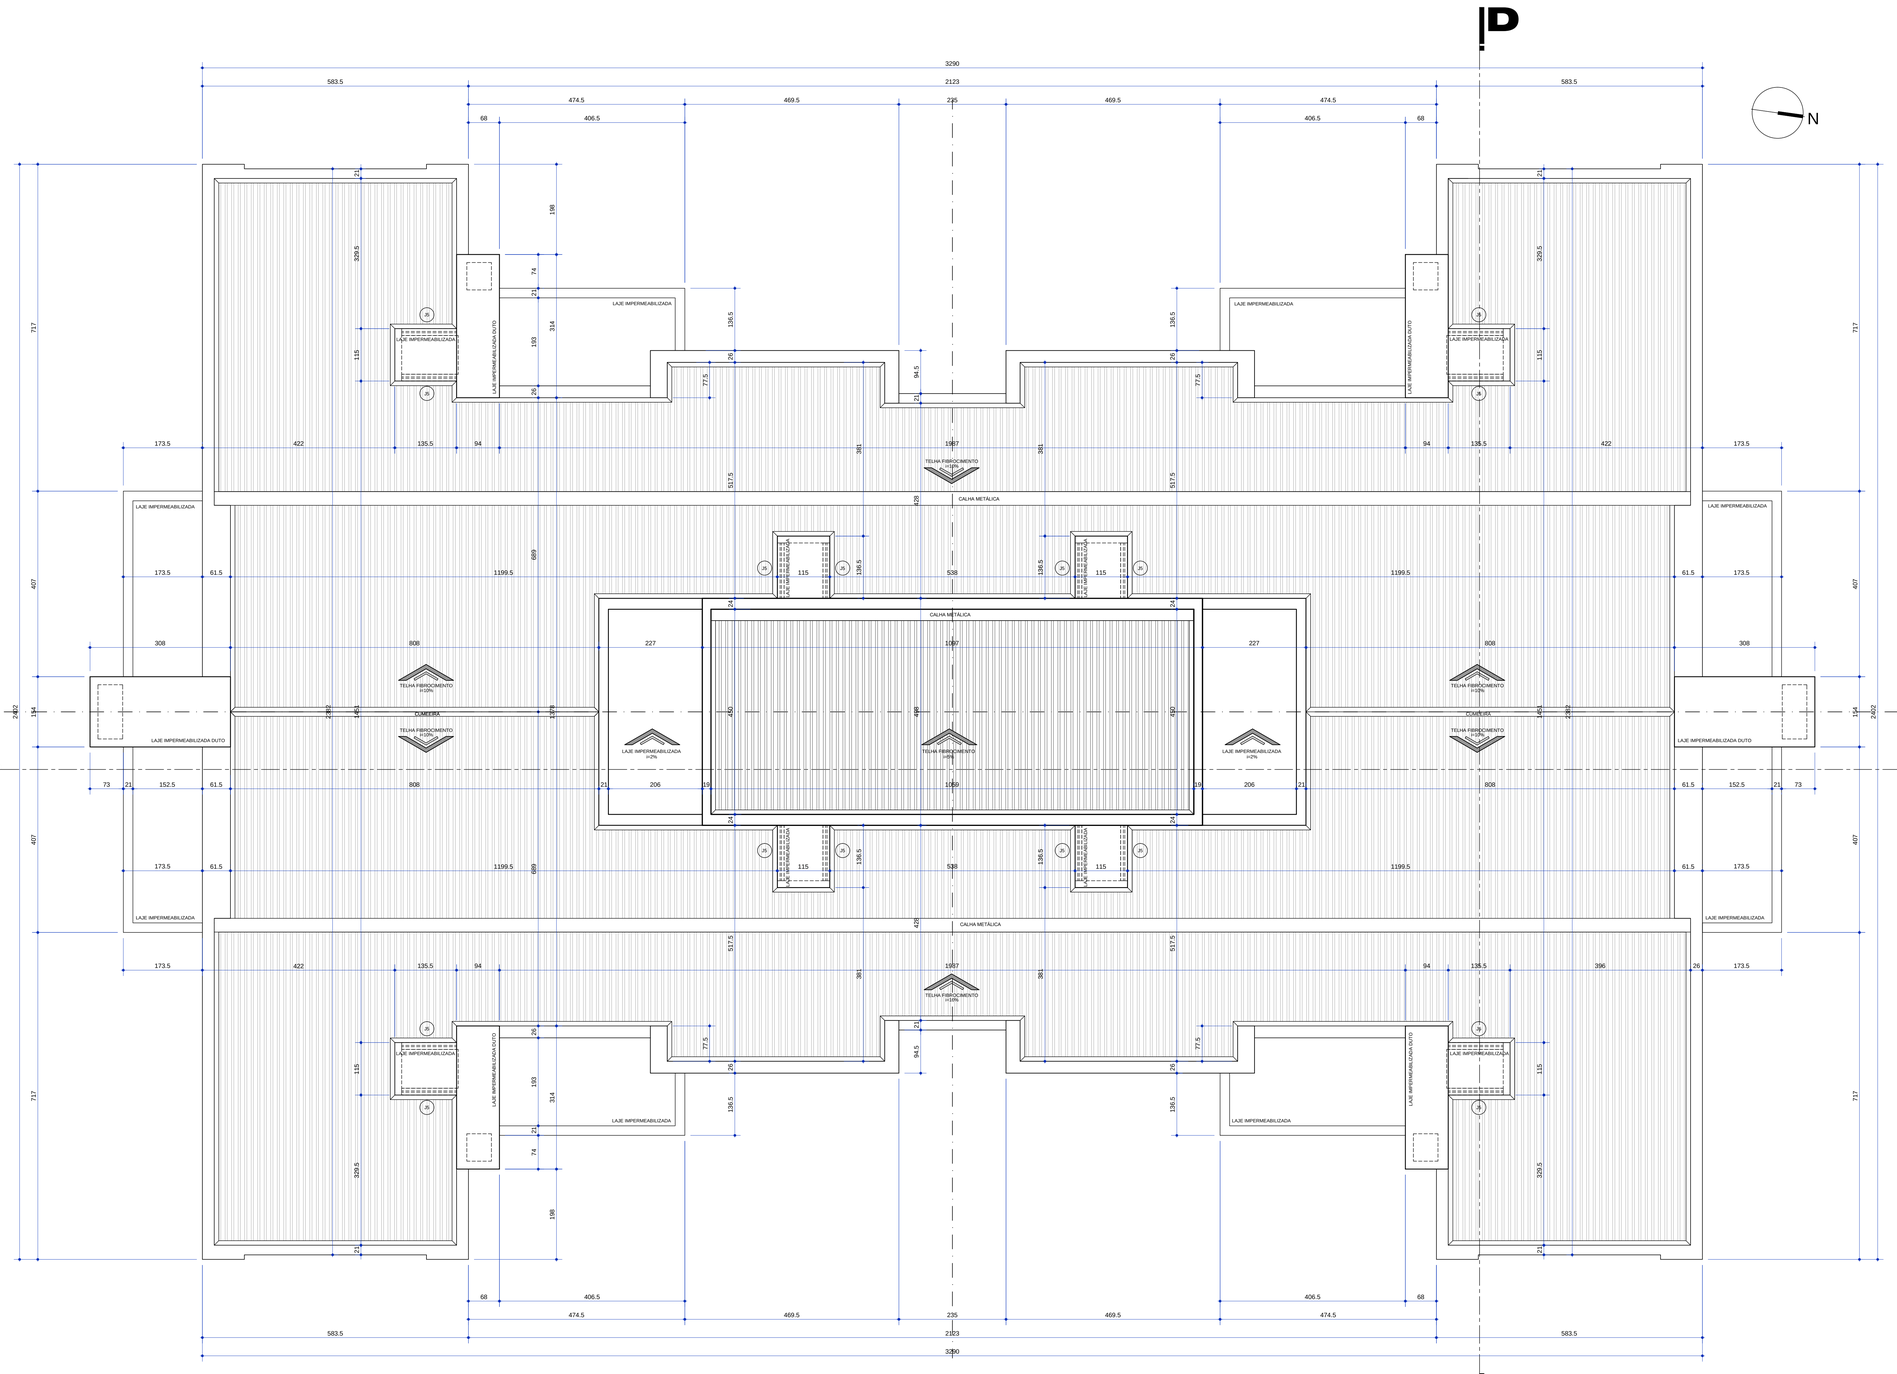

QUADRO DE ESQUADRIAS TORRE RESIDENCIAL

CÓD.	NOMENCL.	LARGURA	ALTURA	PEITORIL	ABERTURA	VIDRO	OBSERVAÇÕES
J1	JANELA ALUMÍNIO	119	105	120	CORRER/VENZ.	INCOLOR	ACABAMENTO ALUMÍNIO ARRANHA-CÉU E750
J2	JANELA ALUMÍNIO	150	105	120	CORRER/VENZ.	INCOLOR	ACABAMENTO ALUMÍNIO ARRANHA-CÉU E750
J3	JANELA ALUMÍNIO	060	065	160	BASCULANTE	VD FANTASIA	ACABAMENTO ALUMÍNIO ARRANHA-CÉU E750
J4	JANELA ALUMÍNIO	058	065	160	BASCULANTE	VD FANTASIA	ACABAMENTO ALUMÍNIO ARRANHA-CÉU E750
J5	JANELA ALUMÍNIO	221	050	-	FIXO	-	TELA ARAME 3MM EM MALHA 2,5X2,5CM
J05	JANELA ALUMÍNIO	120	040	4180	FIXO	-	VENEZIANA ALUMÍNIO ARRANHA-CÉU E750
PM1	PORTA MADEIRA	080	210	-	ABRIR	-	PINTURA COR BRANCO
PM2	PORTA MADEIRA	070	210	-	ABRIR	-	PINTURA COR BRANCO
PM3	PORTA MADEIRA	060	210	-	ABRIR	-	PINTURA COR BRANCO
PJ1	PORTA ALUMÍNIO	296	225	-	CORRER	INCOLOR	ACABAMENTO ALUMÍNIO ARRANHA-CÉU E750
PA1	PORTA ALUMÍNIO	060	190	-	ABRIR	-	ACABAMENTO ALUMÍNIO ARRANHA-CÉU E750
PA2	PORTA ALUMÍNIO	070	140	-	ABRIR	-	ACABAMENTO ALUMÍNIO ARRANHA-CÉU E750
PA3	PORTA ALUMÍNIO	080	100	-	ABRIR	-	ACABAMENTO ALUMÍNIO ARRANHA-CÉU E750
PCF	PORTA CORTA FOGO	090	210	-	ABRIR	-	80 CM DE VÃO LUZ

CONVENÇÕES

BG1 BANCADA GRANITO, H=85 CM
VER DETALHAMENTO

BG2 BANCADA GRANITO, H=92 CM
VER DETALHAMENTO

BG3 BANCADA GRANITO, H=105 CM
VER DETALHAMENTO

REVISÕES

DATA	PROCEDIMENTO
24/07/2023	ENTREGA R00
24/08/2023	ENTREGA R01

MIGUEL VIANI — ARQUITETO E URBANISTA - CAU A267523-3
VITOR GROSSO — ARQUITETO E URBANISTA - CAU A539424-2
RENATO VIANI — ARQUITETO E URBANISTA - CAU A39683-5
viani ARQUITETURA
rua joão wyclif 111 sl 107 : 86050-450 palhano : londrina-pr : (43)3028-3990 : contato@vianiarquitetura.com.br : www.vianiarquitetura.com.br

YTICON CONSTRUÇÃO E INCORPORAÇÃO LTDA.

24 JULHO 2023
LONDRINA-PR
PLA-COBERTURA_TORRE02-R00.dwg

391

TÍTULO DA PRANCHA
PROJETO ARQUITETÔNICO

PLANTA COBERTURA TORRE 02

PRANCHA: PL10 /12

ESCALA: INDICADAS

USO DA EDIFICAÇÃO
CONSTRUÇÃO DE:
EDIFICAÇÃO RESIDENCIAL MULTIFAMILIAR VERTICAL [RMV]

ZONEAMENTO: ZR7

COEF. DE APROVEITAMENTO: 2,91 (MÁX:3,50)

LOCAL DA OBRA
LOTE 101/A, DA SUBDIVISÃO DO LOTE 101 REMANESCENTE, SITUADO NO RIBEIRÃO DA ESPERANÇA, FAZENDA PALHANO, LONDRINA-PR

DATA DO PROJETO: 24/07/2023

TAXA DE OCUPAÇÃO: 61,77% (MÁX: 80%)

PROPRIETÁRIO
YTICON CONSTRUÇÃO E INCORPORAÇÃO LTDA

CNPJ 10.910.748/0001-85

INSCRIÇÃO IMOBILIÁRIA 06020259103960001

SITUAÇÃO SEM ESCALA - VER PRANCHA PL01

DECLARO QUE A APROVAÇÃO DO PROJETO NÃO IMPLICA NO RECONHECIMENTO POR PARTE DA PREFEITURA DO DIREITO DE PROPRIEDADE DO TERRENO.

BRUNO RAFAEL CATARINO:04244617906 — Assinado de forma digital por BRUNO RAFAEL CATARINO:04244617906 Dados: 2023.09.25 16:25:18 -03'00'

PROPRIETÁRIO
YTICON CONSTRUÇÃO E INCORPORAÇÃO LTDA.
CNPJ 10.910.748/0001-85

QUADRO DE ÁREAS [VER QUADRO COMPLETO EM ANEXO NA PRANCHA PL01]

RENATO MATEUS GORNE VIANI:02635778990 — Assinado de forma digital por RENATO MATEUS GORNE VIANI:02635778990 Dados: 2023.08.24 11:23:21 -03'00'

AUTOR DO PROJETO:
RENATO MATEUS GORNE VIANI
ARQUITETO E URBANISTA - CAU A30683-9

IVANI GONCALVES DA SILVA MARIANO:67369553949 — Assinado de forma digital por IVANI GONCALVES DA SILVA MARIANO:67369553949 Dados: 2023.09.25 17:05:37 -03'00'

RESPONSÁVEL TÉCNICO PELA EXECUÇÃO DA OBRA
BRUNO RAFAEL CATARINO
ENGENHEIRO CIVIL - CREA PR-84122/D

ESPAÇO RESERVADO PARA APROVAÇÃO
Assinatura Eletrônica

DIRETORIA APROVAÇÃO DE PROJETOS
Londrina, 22 de setembro de 2023.
Processo Aprovação nº 19.021.125875/2023-06
Nº de ORDEM: 2457/2023
Nº de ALVARÁ: 2457/2023

MARCELO PAGOTTO CARNEIRO
Matrícula nº 13577-1

ESPAÇO RESERVADO PARA APROVAÇÃO (Observações)

MARCELO PAGOTTO CARNEIRO:01643439979 — Assinado de forma digital por MARCELO PAGOTTO CARNEIRO:01643439979 Dados: 2023.09.26 14:17:22 -03'00'